


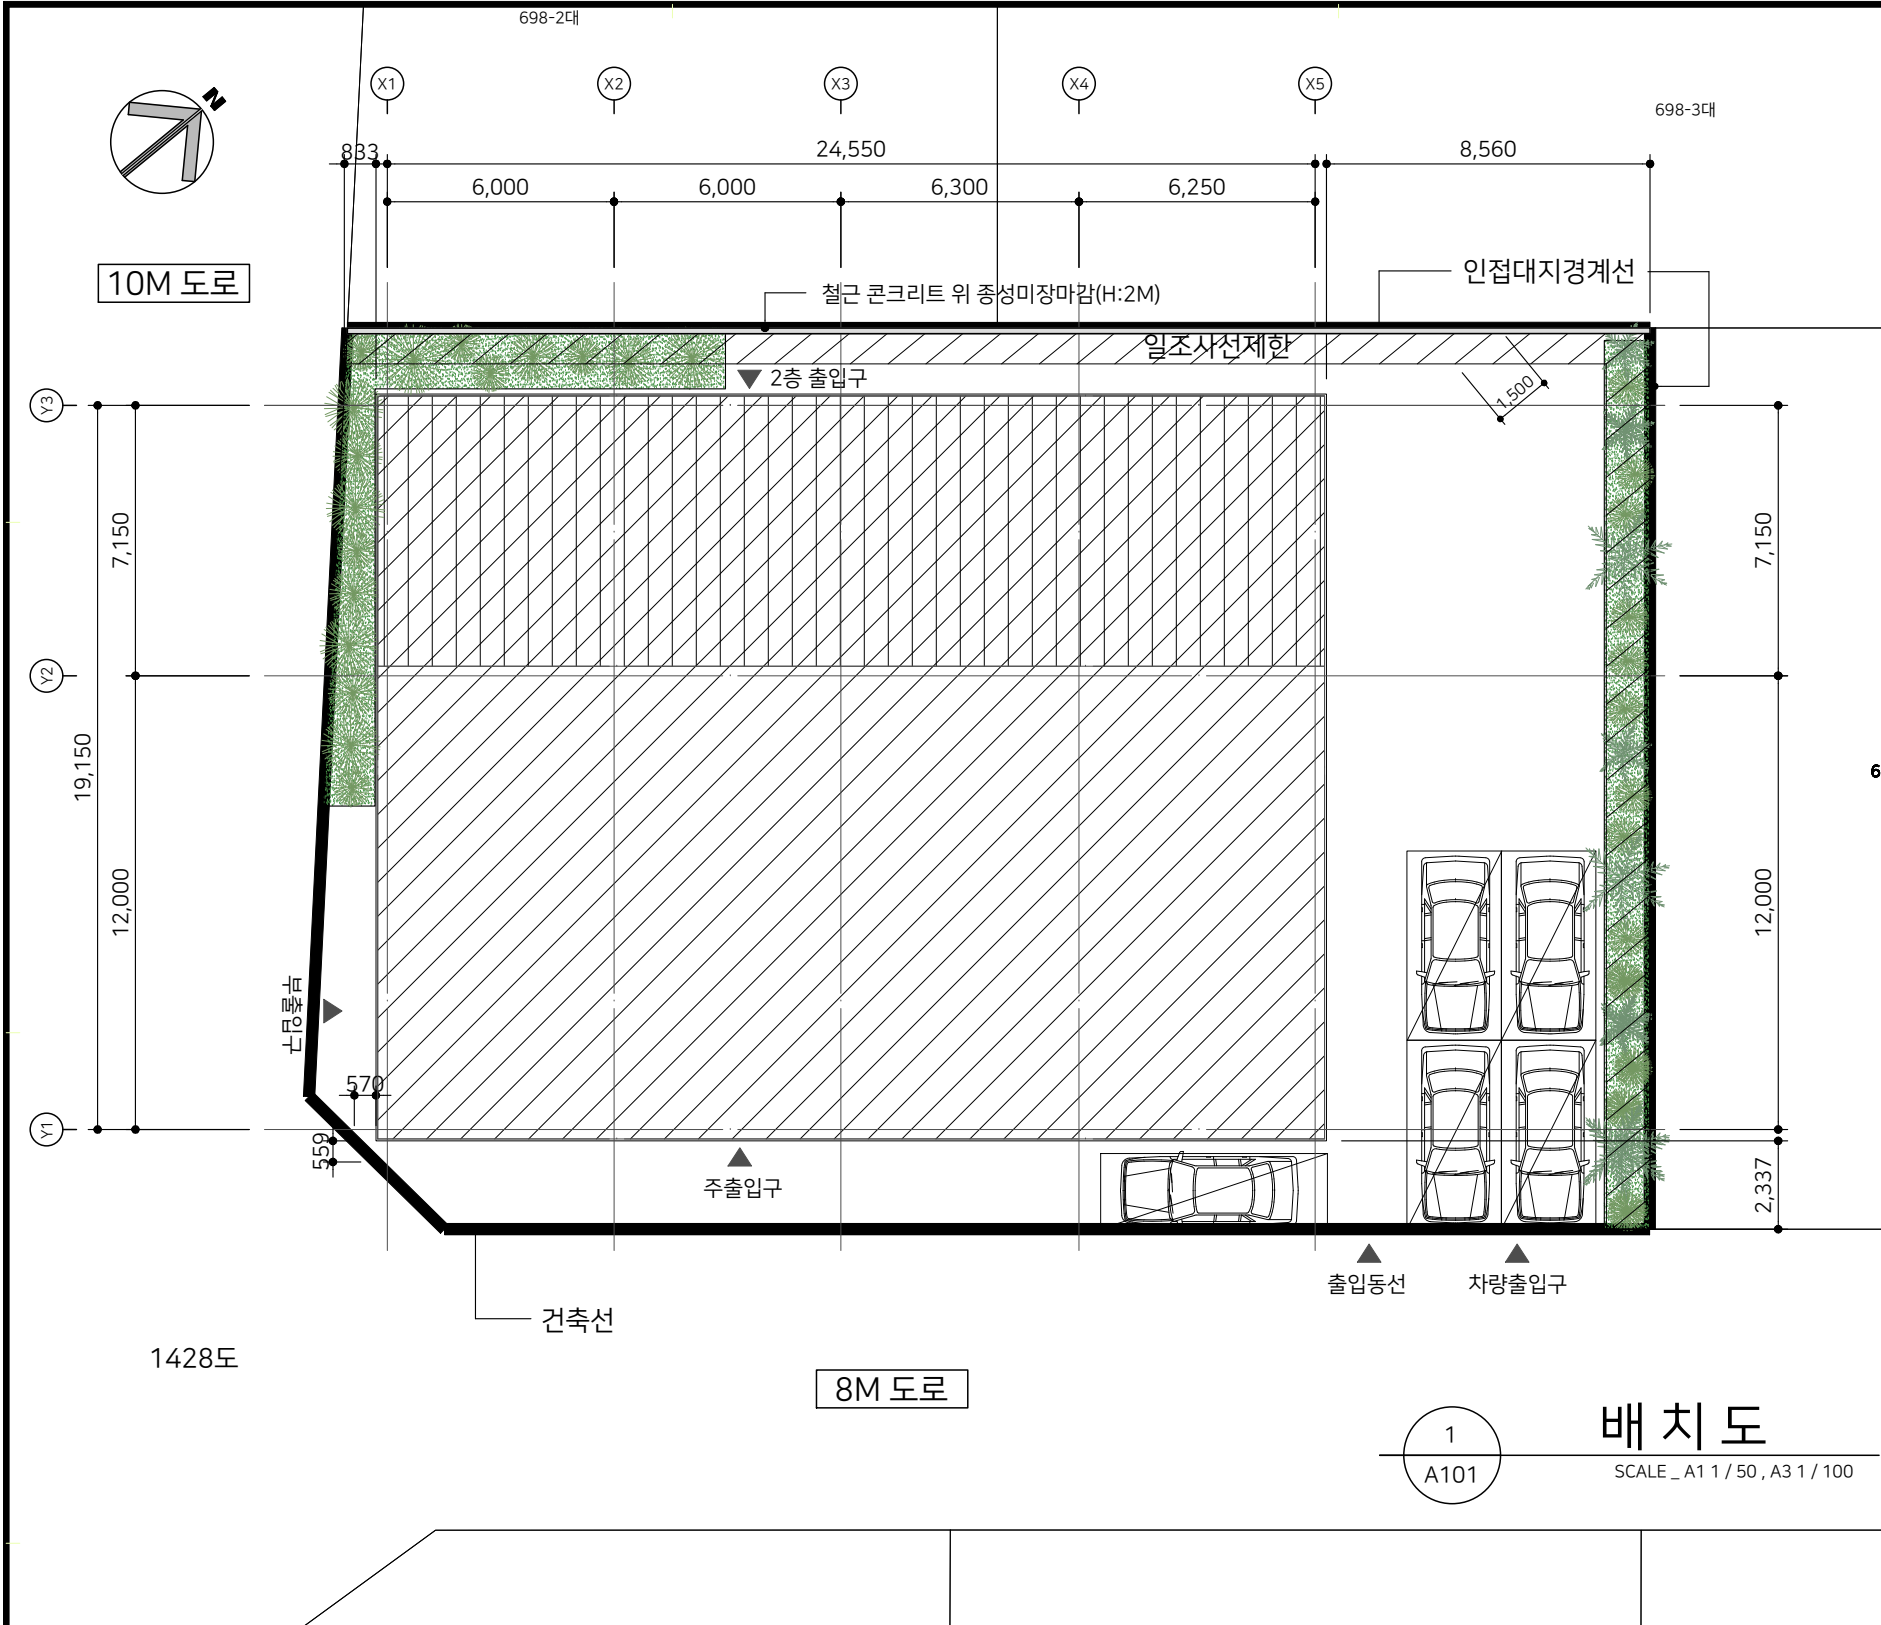

대 지 개 요

대 지 위 치	경상남도 김해시 화목동 698-14
대 지 면 적	829.20 m ²
도로공제면적	0.00 m ²
사용대지면적	829.20 m ²
지역 및 지구	도시지역, 제2종 일반주거지역,가축사육제한구역
전 면 도 로	8M 통과도로
주 차 대 수	8M 통과도로

건 축 개 요

구 분	산 출 근 거	면 적 (m ²)
건 축 면 적	바닥면적산출표 참조	495.73
연 면 적	바닥면적산출표 참조	674.84
용적율연면적	연면적 - (지하층면적+주차장)	674.84
건 폐 율	495.73 / 829.20 x 100	59.78 %
용 적 율	674.84 / 829.20 x 100	81.38 %
층 수	지상 2 층	

층 별 개 요

층 별	용 도	면 적(m ²)
1 층	제2종 근린생활시설(수리점)	495.73
2 층	제2종 근린생활시설(사무실)	179.11
합 계		674.84

범 례	주차 대수 산출	조경 면적 산정	정화조인원 및 오수량산출	장애인 편의시설 설치 검토
사용대지 건축면적 조경구간	1 층 2 층 * 김해시 주차장 설치 및 관리 조례 [별표6] - 근린생활시설 시설면적 150m² 당 1대 근린생활시설 674.84m²... 674.84/150 = 4.50 * 법정 주차대수 : 5대 / 설계 주차대수 : 5대 설치	* 건축법 제42조 대지의 조경 대지면적 200m² 이상으로서, 연면적이1,000m² 미만은 대지면적의 5% 이상조경이나 그 밖에 필요한 조치를 하여야 한다. 법정조경면적 : 829.20m² x 0.05 =41.46m² * 계획조경면적 : 56.21m²	* 오수발생량 산출기준 수리점 15 L / m² = 0.005 x 495.73 = 2.479m³ 사무실 15 L / m² = 0.015 x 179.11 = 2.687m³ 2.479 + 2.687 = 5.166 m³/DAY * 5.166 m³/DAY 미만 이므로 원인자부담금 제외 대상.	* 장애인·노인·임산부 등의 편의증진보장에 관한 법률 시행령 [별표1] 편의시설 설치 대상시설 * 제2종 근린생활시설(수리점)(사무실) ... 비대상

PROJECT TITLE
신진유압
신축공사

PROJECT NO.


부산광역시 사하구 하단동 476
TEL . 051 . 791 . 0201
FAX . 051 . 791 . 0203

NOTE

NO. REVISIONS / ISSUE

ARCHITECTURE DESIGNED BY

STRUCTURE DESIGNED BY

MECHANICAL DESIGNED BY


DRAWN BY

CHECKED BY

APPROVED BY

NAME OF DRAWING
건축개요 및 배치

SCALE
A1 SIZE
A3 SIZE 1 /
DATE 2026
DRAWING NO.
A001

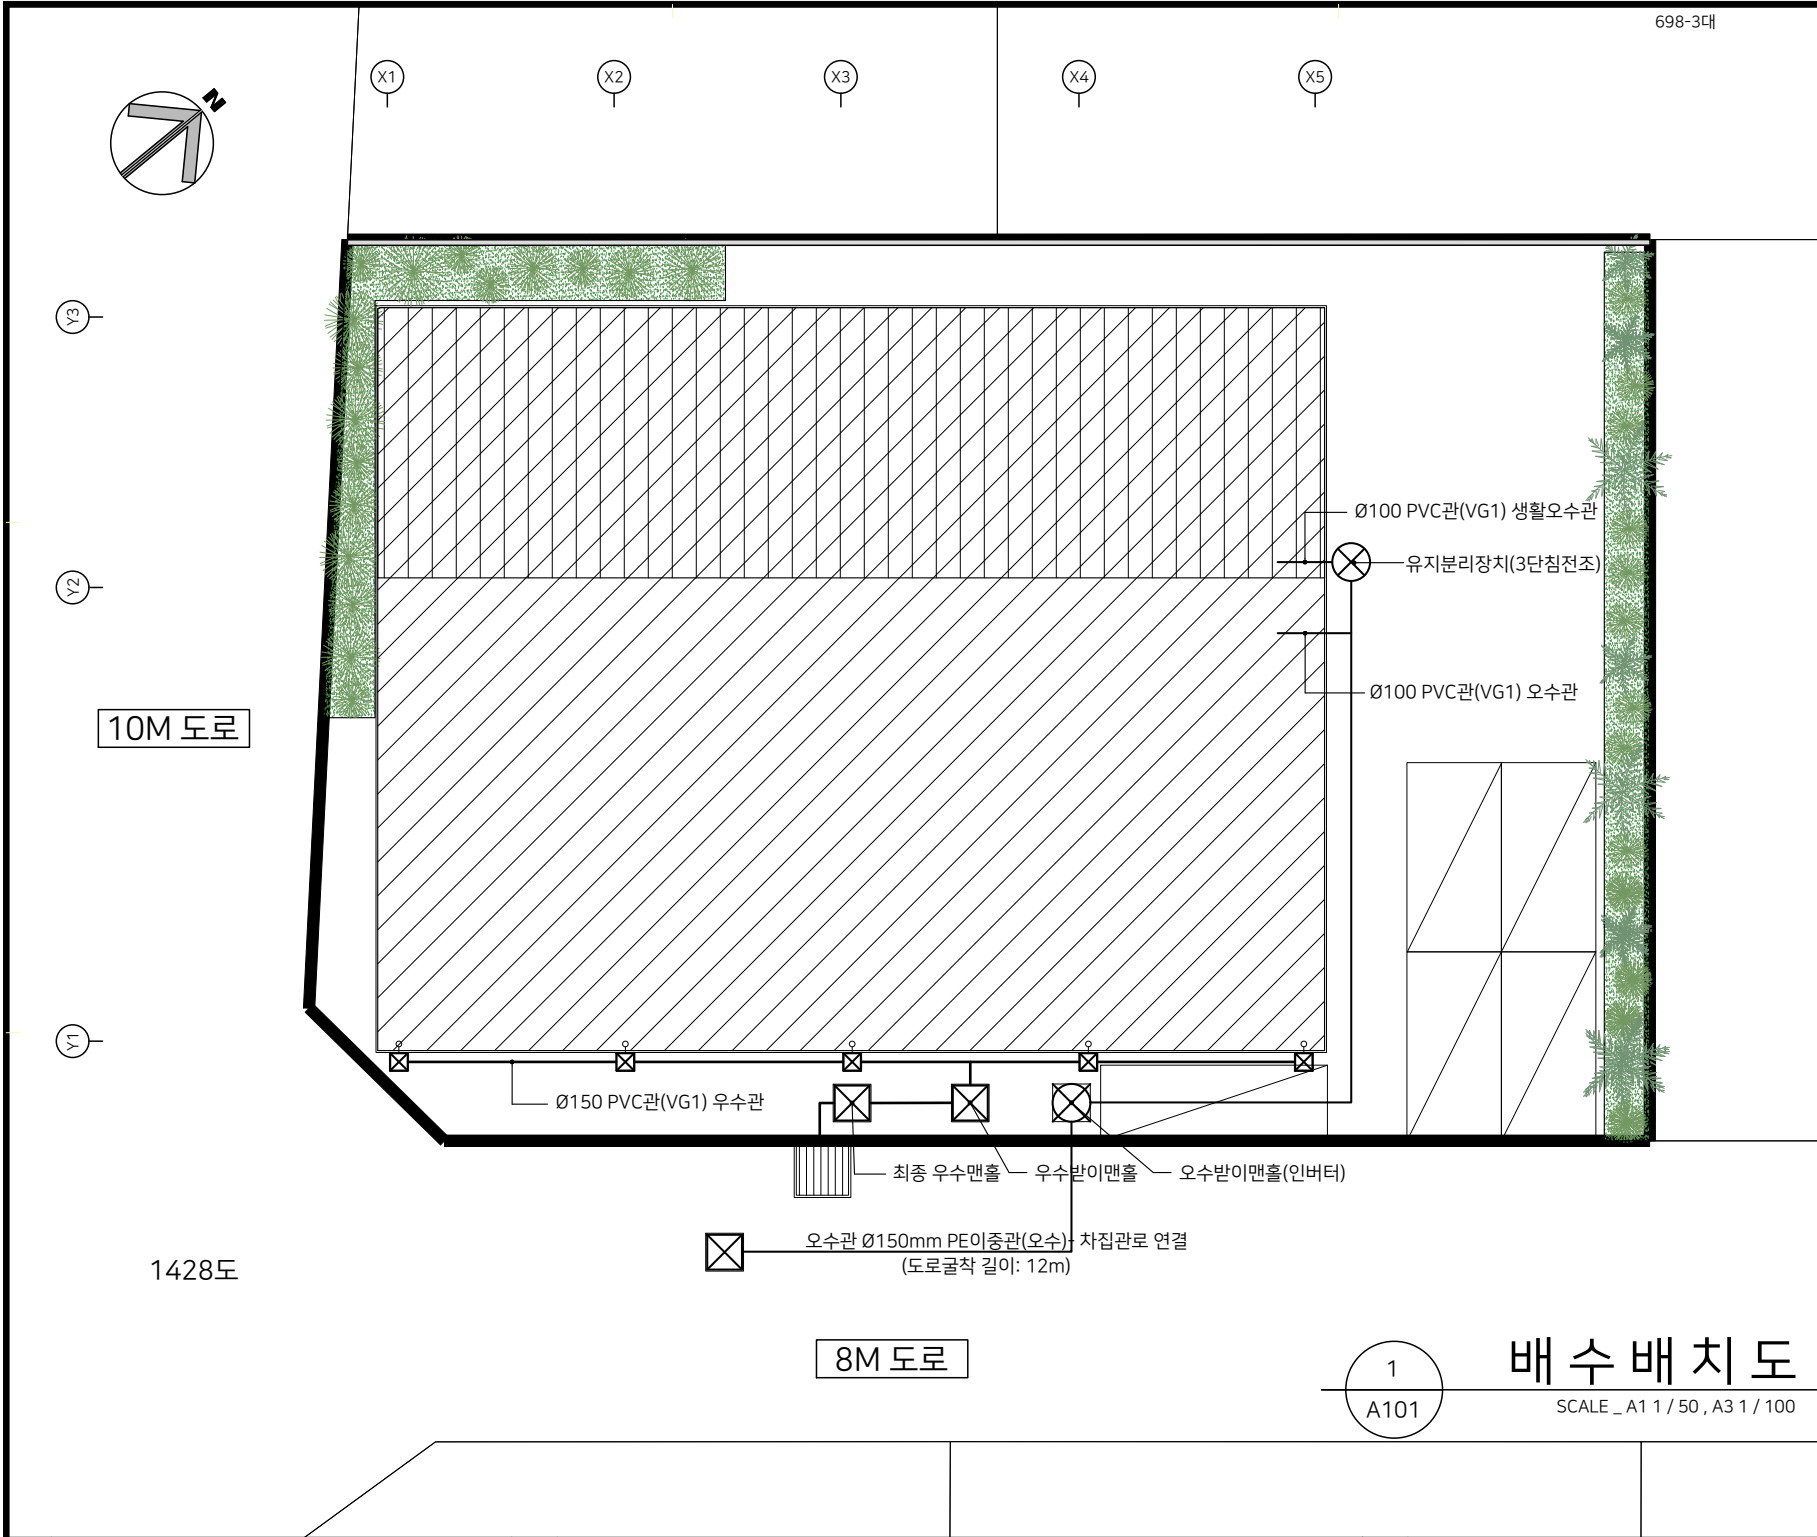

범례

사용대지

도로

Ø100 PVC관(VG1) 우수관

Ø100 PVC관(VG1) 생활우수관

Ø150 PVC관(VG1) 우수관

우수량산출



*우수발생량 산출기준

수리점 15 L / m² = 0.005 x 495.73 = 2.479m³

사무실 15 L / m² = 0.015 x 179.11 = 2.687m³

2.479 + 2.687 = 5.166 m³/DAY

* 5.166 m³/DAY 미만 이므로 원인자부담금 제외 대상.

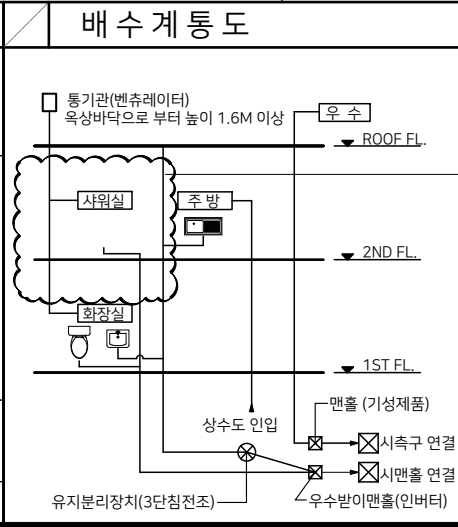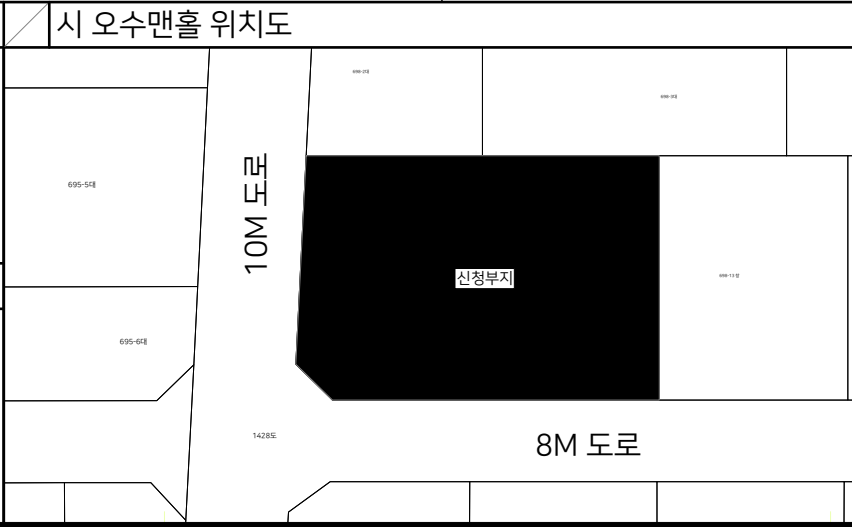

배수 설치 시방서

1. 본 공사는 도면 및 시방서에 의하여 시공하도록하며, 기타 의문사항은 감리자의 지시에 따른다.

2. 공공하수도의 연결은 감리건축사의 입회하여 시공하며, 준공검사시 대지내 맨홀설치 완료후 공공하수도와와 연결접속된 시공상태를 사진촬영하여 준공검사시 제출하도록 한다.

3. 대지내 맨홀과 공공하수맨홀의 연결시 굴착후 원상복구에 철저를 기하며 되메우기 시에는 반드시 다짐하여 침하가 생기지 않도록 한다.

4. 생활우수(주방싱크대,세면대,욕실바닥,발코니바닥)는 우수맨홀에 연결시공하고 우수(지붕빗물및 대지내 바닥배수)는 우수맨홀에 연결시공 하도록 한다.

5. 배수설비설치 시공시 관재질은 p.v.c를 사용하거나 동등 이상의 품질이 인정되는 KS품을 사용한다.

6. 우수맨홀의 두께는 콘크리트 또는 주철재의 밀폐두께로 하며, 우수맨홀의 두께는 우수의 유입이 가능하도록 구멍이 뚫린 주철재 두께로 시공한다.

7. 배수설비설치시 착공예정일 20일전에 필히 구두또는 서면으로 신고하여야 하며, 허가청의 확인을 받아야 한다.

8. 도면에 의한 시공으로 공사에 안전을 기할것이며, 상기 사항을 미이행시에는 재시공은 물론 하수도법 제 37조및 제43조의 규정에 의하여 위법 조치 되오니 양지 하시기 바랍니다.

오수맨홀 시방서

가. 최종오수맨홀

: 부지 내 최종 방류구에는 오수맨홀을 설치하여 변기의 오수와 생활하수를 차집하고, 스크린(30mm이하)을 설치하여 부유물이 공공오수본관으로 유입되지 않도록 하여야 하며, 오수맨홀 설치시에는 주변마당의 빗물이 유입되지 않도록 맨홀테두리를 주변 지반보다 5cm이상 높게 시공하고, 빗물의 유입이 없게 밀폐형 두께로 시공하고, 차량의 통행에 지장없게 오수맨홀 덮개(주철제품)를 설치한다.

나. 새들분기관

: 부지 내의 최종 오수맨홀에서 시 오수맨홀에 연결이 부득이 할 시에는 사전에 우리시 (하수과)와 협의하여야 하며, 부득이 할 시 사전에 우리시 (하수과)와 협의하여야 우수본관의 상단부에 천공기로 천공 후 새들분기관을 사용하여 연결관이 본관에 돌출되어 막히는 경우가 없도록 시공한다.

다 . 우수관, 우수관 관중(정확히 기입)

1. 차량 통행하는 곳 - pvc(vg1)관, 이중벽 PE관 / 2. 차량 통행 없는 곳 - pvc(vg2)관 강도 이상의 관 (단 차량이 통행하는 곳에서 pvc(vg2)관을 쓸 경우에는 학술적(역학적) 산출근거를 제출하십시오)

우수관 관경선정

배수설비의 세부설치기준(제23조 제2항 관련)

관경 결정

합류관 및 우수관의 크기는 공공하수도관리청이 특별한 사유가 있다고 인정하는 경우를 제외하고는 다음표와 같다.

단, 우수관의 지관으로서 연장이 3m미만의 것은 관의 지름이 75mm의 것을 사용할 수 있다.

배수면적(m2)	200미만	600미만	1,200미만	1,200이상
안지름(mm)	100이상	150이상	200이상	좌측의 율로 관의 지름 또는 갯수를 증가한다.

오수관 관경선정

관경 결정

오수관의 크기는 공공하수도관리청이 특별한 사유가 있다고 인정하는 경우를 제외하고는 다음 표에 의한다.

단, 우수일부를 배제하기위한 지관으로서 연장이 3m미만의 것의 관의 지름은 75mm의 것을 사용할 수 있다.

배수인구(명)	150이하	300이하	600이하	1,000이하				
관의지름(mm)	100이상	150이상	200이상	250이상				

배수설비의 세부설치기준(제23조 제2항관련)


배수량이 특히 많은 장소에서의 관의 크기는 다음 표에 의한다.

배수량(m3)	1,000미만	2,000미만	4,000미만	6,000미만	6,000이상
관의지름(mm)	150이상	200이상	250이상	300이상	좌측의 율로 관의 지름 또는 갯수를 증가한다.

* 관거의 경사는 관거내 유속이 초당 0.6내지 1.5m가 되어야 한다.

* 배수관 또는 배수거의 기점, 종점, 합류점, 굴곡점 및 안지름 또는 안폭이나 관의 종류가 달라지는 곳에는 물받이를 설치하여야 하며, 배수관 또는 배수거나 직선인 부분에는 안지름 또는 안폭의 120배이하의 간격으로 물받이를 설치하여야 한다.

* 고품물질을 배제하는 유출구에는 유효간격 10mm이하의 스크린을 설치하여야 하며, 유지류를 배제하는 유출구에는 유지차단장치를, 다량의 토사를 배제하는 유출구에는 적당한 크기의 모래받이를 각각 설치하여야 하며, 배수관 또는 배수거의 필요한 부분에는 악취방지트랩을 설치하여야 한다.

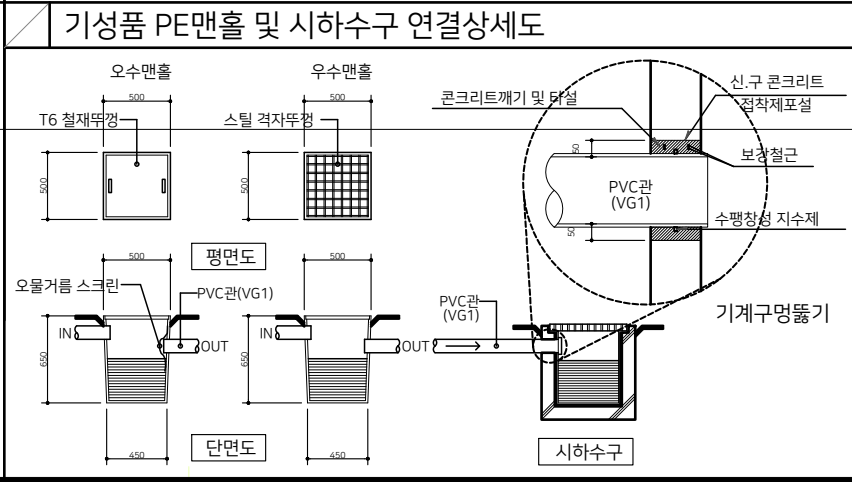

PROJECT TITLE

신진유압
신축공사

PROJECT NO.

지음
건축사사무소
Architects & Interio

부산광역시 사하구 하단동 476

TEL . 051 . 791 . 0201

FAX . 051 . 791 . 0203

NOTE

NO.	REVISIONS / ISSUE	

ARCHITECTURE DESIGNED BY

STRUCTURE DESIGNED BY

MECHANICAL DESIGNED BY

DRAWN BY

CHECKED BY

APPROVED BY

NAME OF DRAWING

배수배치도

SCALE

A1 SIZE

A3 SIZE 1 /

DATE 2022

DRAWING NO.

A001

조경 면적 계획의 법적기준


(단위 : m²)

대 지 위 치	경상남도 김해시 화목동 698-14		관 계 법 령
지 역 지 구	도시지역, 제2종일반주거지역		
대 지 면 적	829.20 m ²		
조경의무면적	법 정	1000m ² 미만, 대지면적의 5%이상 식재	김해시 건축조례 제25조
		$829.20 \times 0.05 = 41.46$	(대지안의 조경)1항1호
	계 획	56.21 m ²	
식재의무면적	법 정	조경의무면적의 50%이상	국토교통부 고시 제4조
		$41.46 \times 0.50 = 20.73$	
	계 획	30.00 m ²	
자연지반	법 정	조경의무면적의10%이상	국토교통부 고시 제5조
		$41.46 \times 0.10 = 4.15$	
	계 획	4.80 m ²	

조경면적표

(단위 : m²)

구 분	분 류	산출근거	면 적	비 고
지상조경	①	CAD 산출	28.01	
	②	CAD 산출	28.20	
	합 계	28.01+28.20	56.21	
조경의무면적	829.20 X 0.05		41.46	대지면적의 5%이상 식재
식재의무면적	41.46 X 0.50		20.73	조경의무면적의 50%이상
자연지반	41.46 X 0.10		4.15	조경의무면적의10%이상

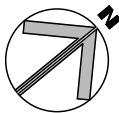

12,639.56

1,360

428도

698-2대

28.01 m²

698-3대

10,000

590

1,200

23,500

PROJECT TITLE

신진유압
신축공사

PROJECT NO.



부산광역시 사하구 하단동 476
TEL . 051 . 791 . 0201
FAX . 051 . 791 . 0203

NOTE

NO.	REVISIONS / ISSUE	

ARCHITECTURE DESIGNED BY

STRUCTURE DESIGNED BY

MECHANICAL DESIGNED BY

DRAWN BY

CHECKED BY

APPROVED BY

NAME OF DRAWING

조경 개요/ 조경면적

SCALE

A1 SIZE

A3 SIZE

DATE

DRAWING NO.

L001

조경 식재 계획의 법적기준



교 목		법 정	조경의무면적의 ㎡ 당 0.2주 이상	국토교통부 고시 제7조
			41.46 X 0.2 = 8.29주 (9주)	(주거지역)
		계 획	10?	
관 목		법 정	조경의무면적의 ㎡ 당 1.0주 이상	국토교통부 고시 제7조
			41.46 X 1.0 = 41.46주 (42주)	(주거지역)
		계 획	100?	
상록비율	상록교목	법 정	교목수량의 20%이상	국토교통부 고시 제8조
			8.29 X 0.2 = 1.66주 (2주)	1. 상록수 식재비율
	계 획	5?		
	상록관목	법 정	관목수량의20%이상	국토교통부 고시 제8조
			41.46 X 0.2 = 8.29주 (9주)	1. 상록수 식재비율
계 획		50?		
기 타		법 정	지역특성수 : 교목의 10%식재	국토교통부 고시 제8조
			8.29 X 0.1 = 0.83주 (1주)	2.지역에 따른 특성수종 식재비율
		계 획	5?	시목 : 동백나무

식재수량표

성 상	분 류	기 호	수 종	규 격	수량	인정수량	단위	비 고
교 목	상록교목	●	동백나무	H2.5xR6	5	5	주	
			소 계		5	5	주	
	낙엽교목	○	청단풍	H2.0xR6	5	5	주	
			소 계		5	5	주	
	교목계				10	10	주	
관 목	상록관목	■	회양목	H0.3xW0.3	50	50	주	
			소 계		50	50	주	
	낙엽관목	■	남천	H1.0x3가지	50	50	주	
			소 계					
	관목계				100	100	주	
기 타	지 피	■	별아이비	4치포트	120	120	본	

시설물/포장 수량표

구 분	기 호	시 설 명	규 격	단위	수량	비 고
시설물	■■■■■	화강석 경계석	W100 x H0.1M	M	12.00	
	■■■■■	플랜터 B	W100 x H0.4M	M	15.40	건축주지정플랜터
포 장		인조화강석블럭	200x200xT60	M2	12.50	건축주지정블럭
배 수		내압투수판	T30 /2겹	M2	12.50	
		투수슈트	T5/M	M2	17.12	벽 감아올리기(H=0.3M)

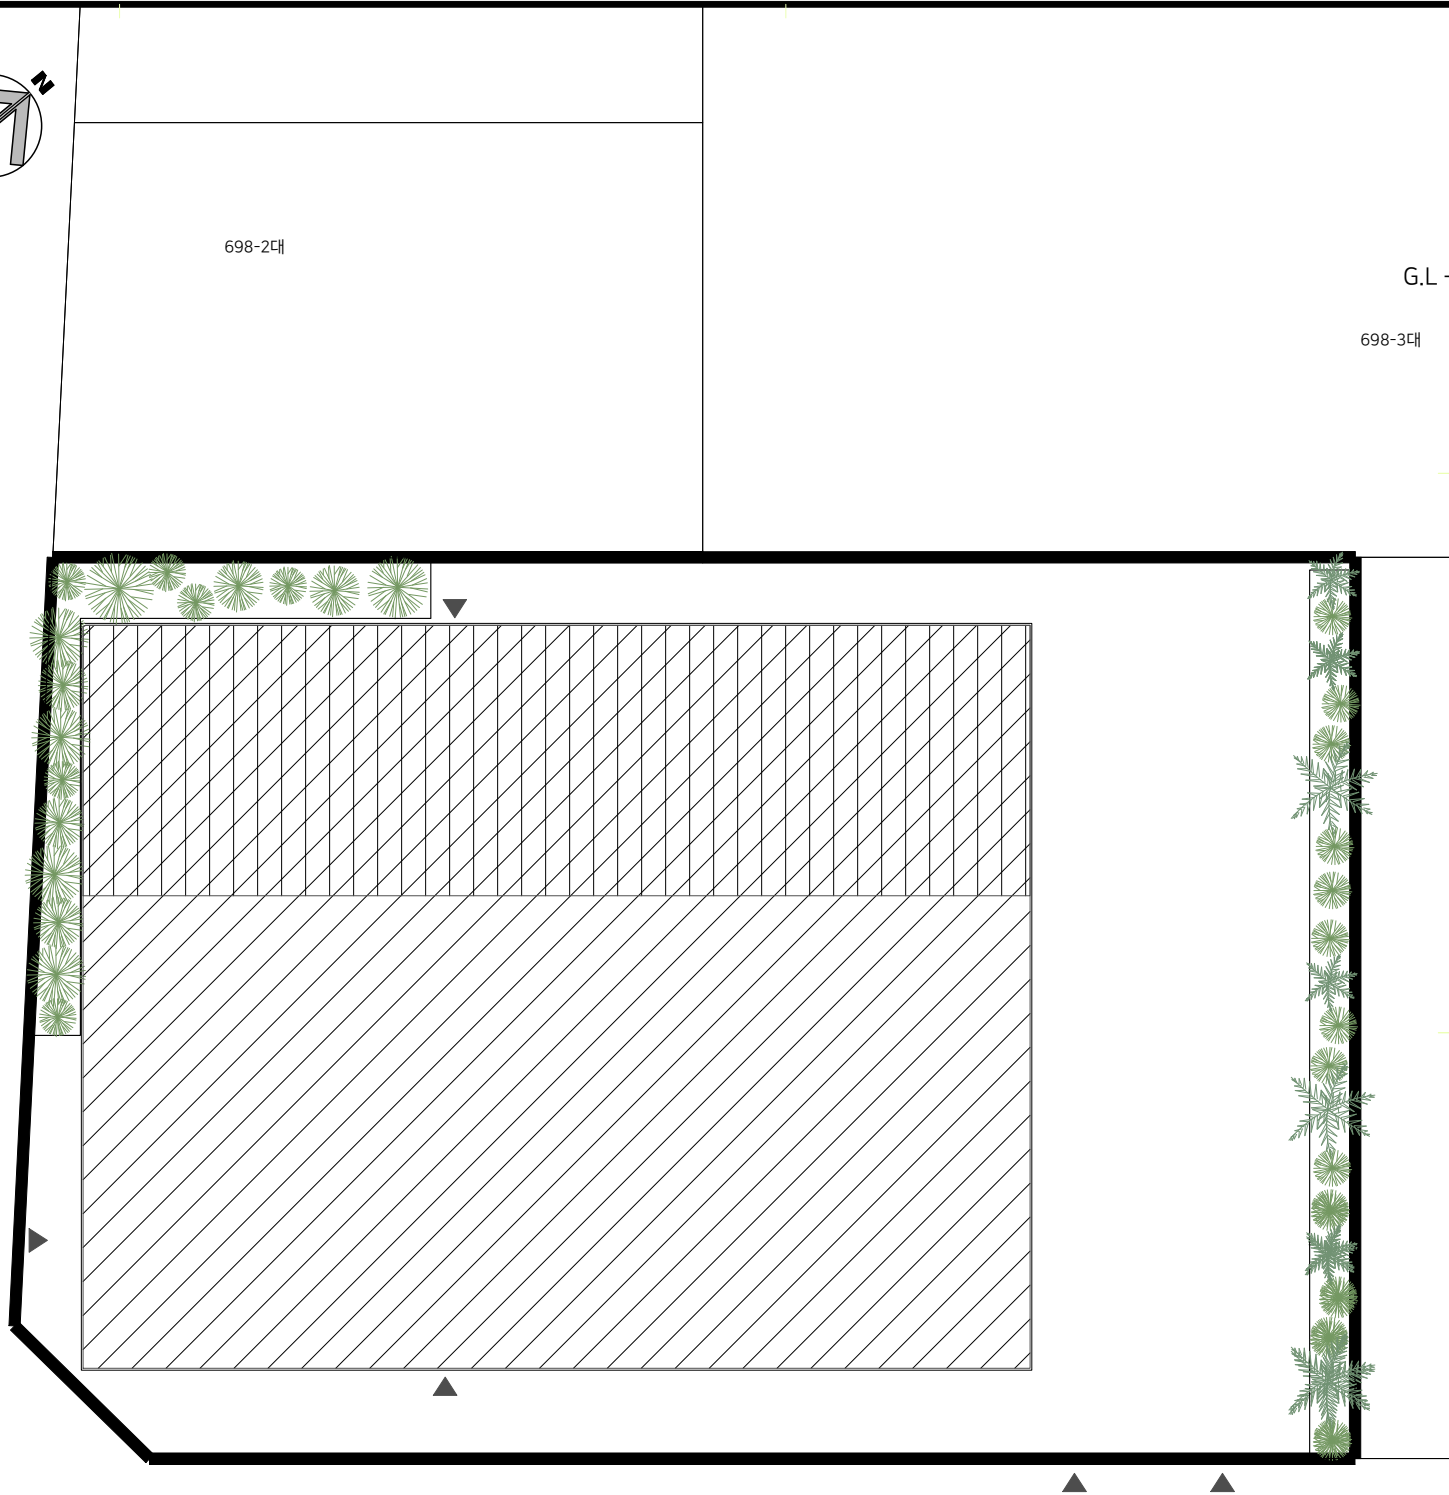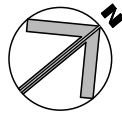

PROJECT TITLE
신진유압
신축공사

PROJECT NO.

G.L 1,000
698-3대

부산광역시 사하구 하단동 476
TEL . 051 . 791 . 0201
FAX . 051 . 791 . 0203

- NOTE
- 1.조형플랜터 겸 벤치 설치시
포장 마감 후 제품 설치
- 2.건축공사
:배수공사
(표면배수, 심토층배수,트랜치
:방근공사
(건축슬라브 상부 방수 방수 시 방근
포함하여 계획)
:구조물공사
(식재플랜터 구성을 위한 콘크
구체공사)

NO.	REVISIONS / ISSUE	

ARCHITECTURE DESIGNED BY

STRUCTURE DESIGNED BY

MECHANICAL DESIGNED BY

DRAWN BY

CHECKED BY


APPROVED BY

NAME OF DRAWING

조경 식재 배식계획

SCALE
A1 SIZE
A3 SIZE 1 /
DATE 2021
DRAWING NO.

L002

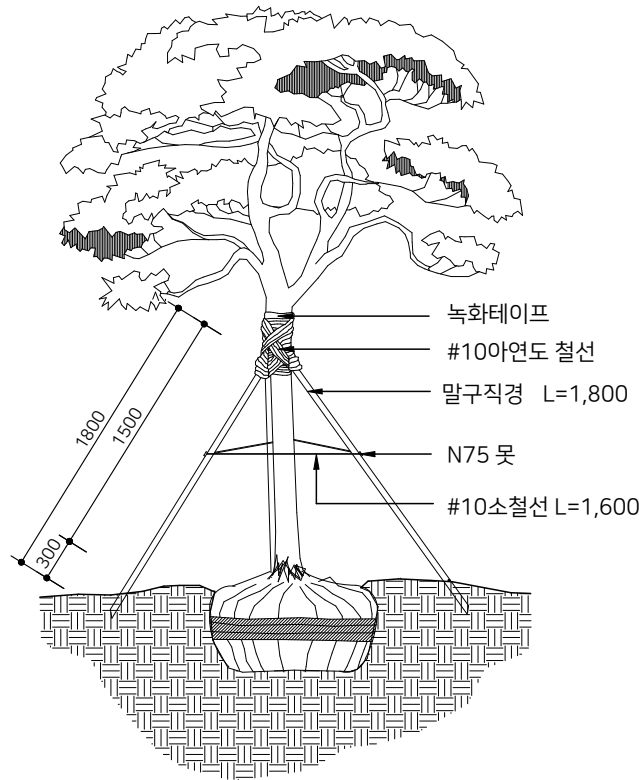


지주별 설치 상세도

1

L00

SCALE _ 1/NONE

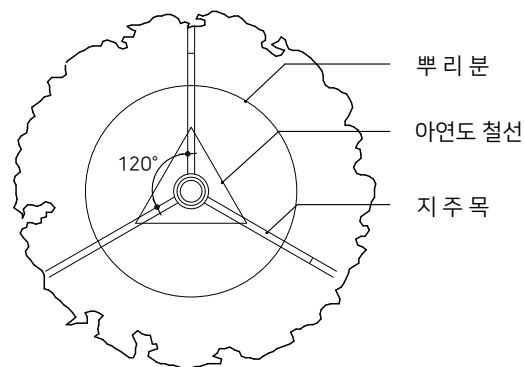


지주별 설치 평면도


3

L00

SCALE _ 1/NONE

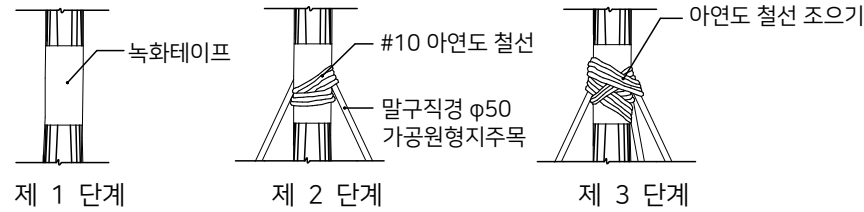

주) 지주목으로 사용하는 통나무는 완전박피해야 하며 미관을 고려
방향 및 높이를 일정하게 하며 수목이 흔들리지 않도록 단단히 결속할 것.
수간과 접촉되는 부분은 삼발이를 가공하여 완전 밀착되도록 할 것.

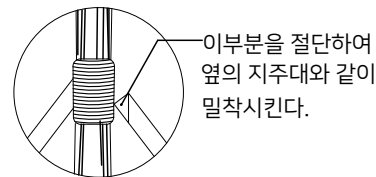


새끼감기 표준 상세도

2

L00

SCALE _ 1/NONE

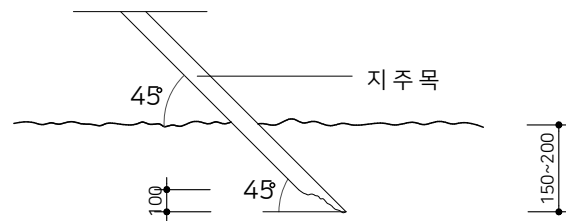


지주목 지하 매설물 부분 상세도

4

L00

SCALE _ 1/NONE

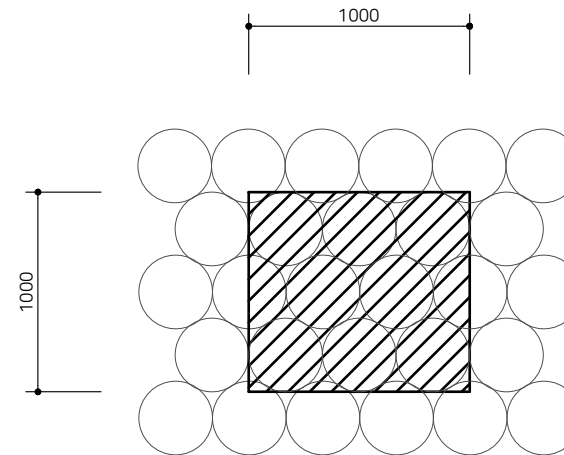


관목 W0.3인 수종 16주/㎡
W0.4인 수종 12주/㎡
W0.6인 수종 8주/㎡

관목(군식)식재 패턴 상세도

5

L00

SCALE _ 1/NONE

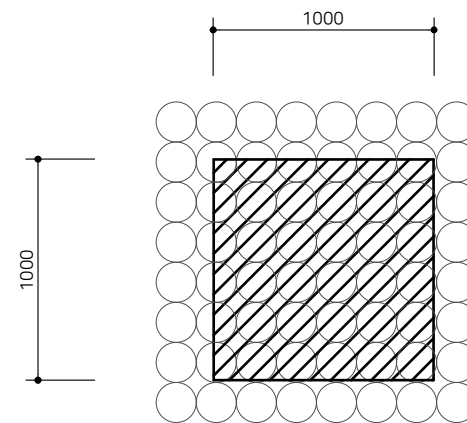

지피류 25본/㎡

초화류(군식) 식재 패턴 상세도

6

L00

SCALE _ 1/NONE

PROJECT TITLE

화목동 698-14
신축계획안

PROJECT NO.



부산광역시 사하구 하단동 476
TEL . 051 . 791 . 0201
FAX . 051 . 791 . 0203

NOTE

NO.	REVISIONS / ISSUE

ARCHITECTURE DESIGNED BY

STRUCTURE DESIGNED BY

MECHANICAL DESIGNED BY

DRAWN BY

CHECKED BY

APPROVED BY

NAME OF DRAWING

지주목/식재패턴 상

SCALE

A1 SIZE


A3 SIZE

DATE

DRAWING NO.

L003

인공지반 부분 단면 상세도

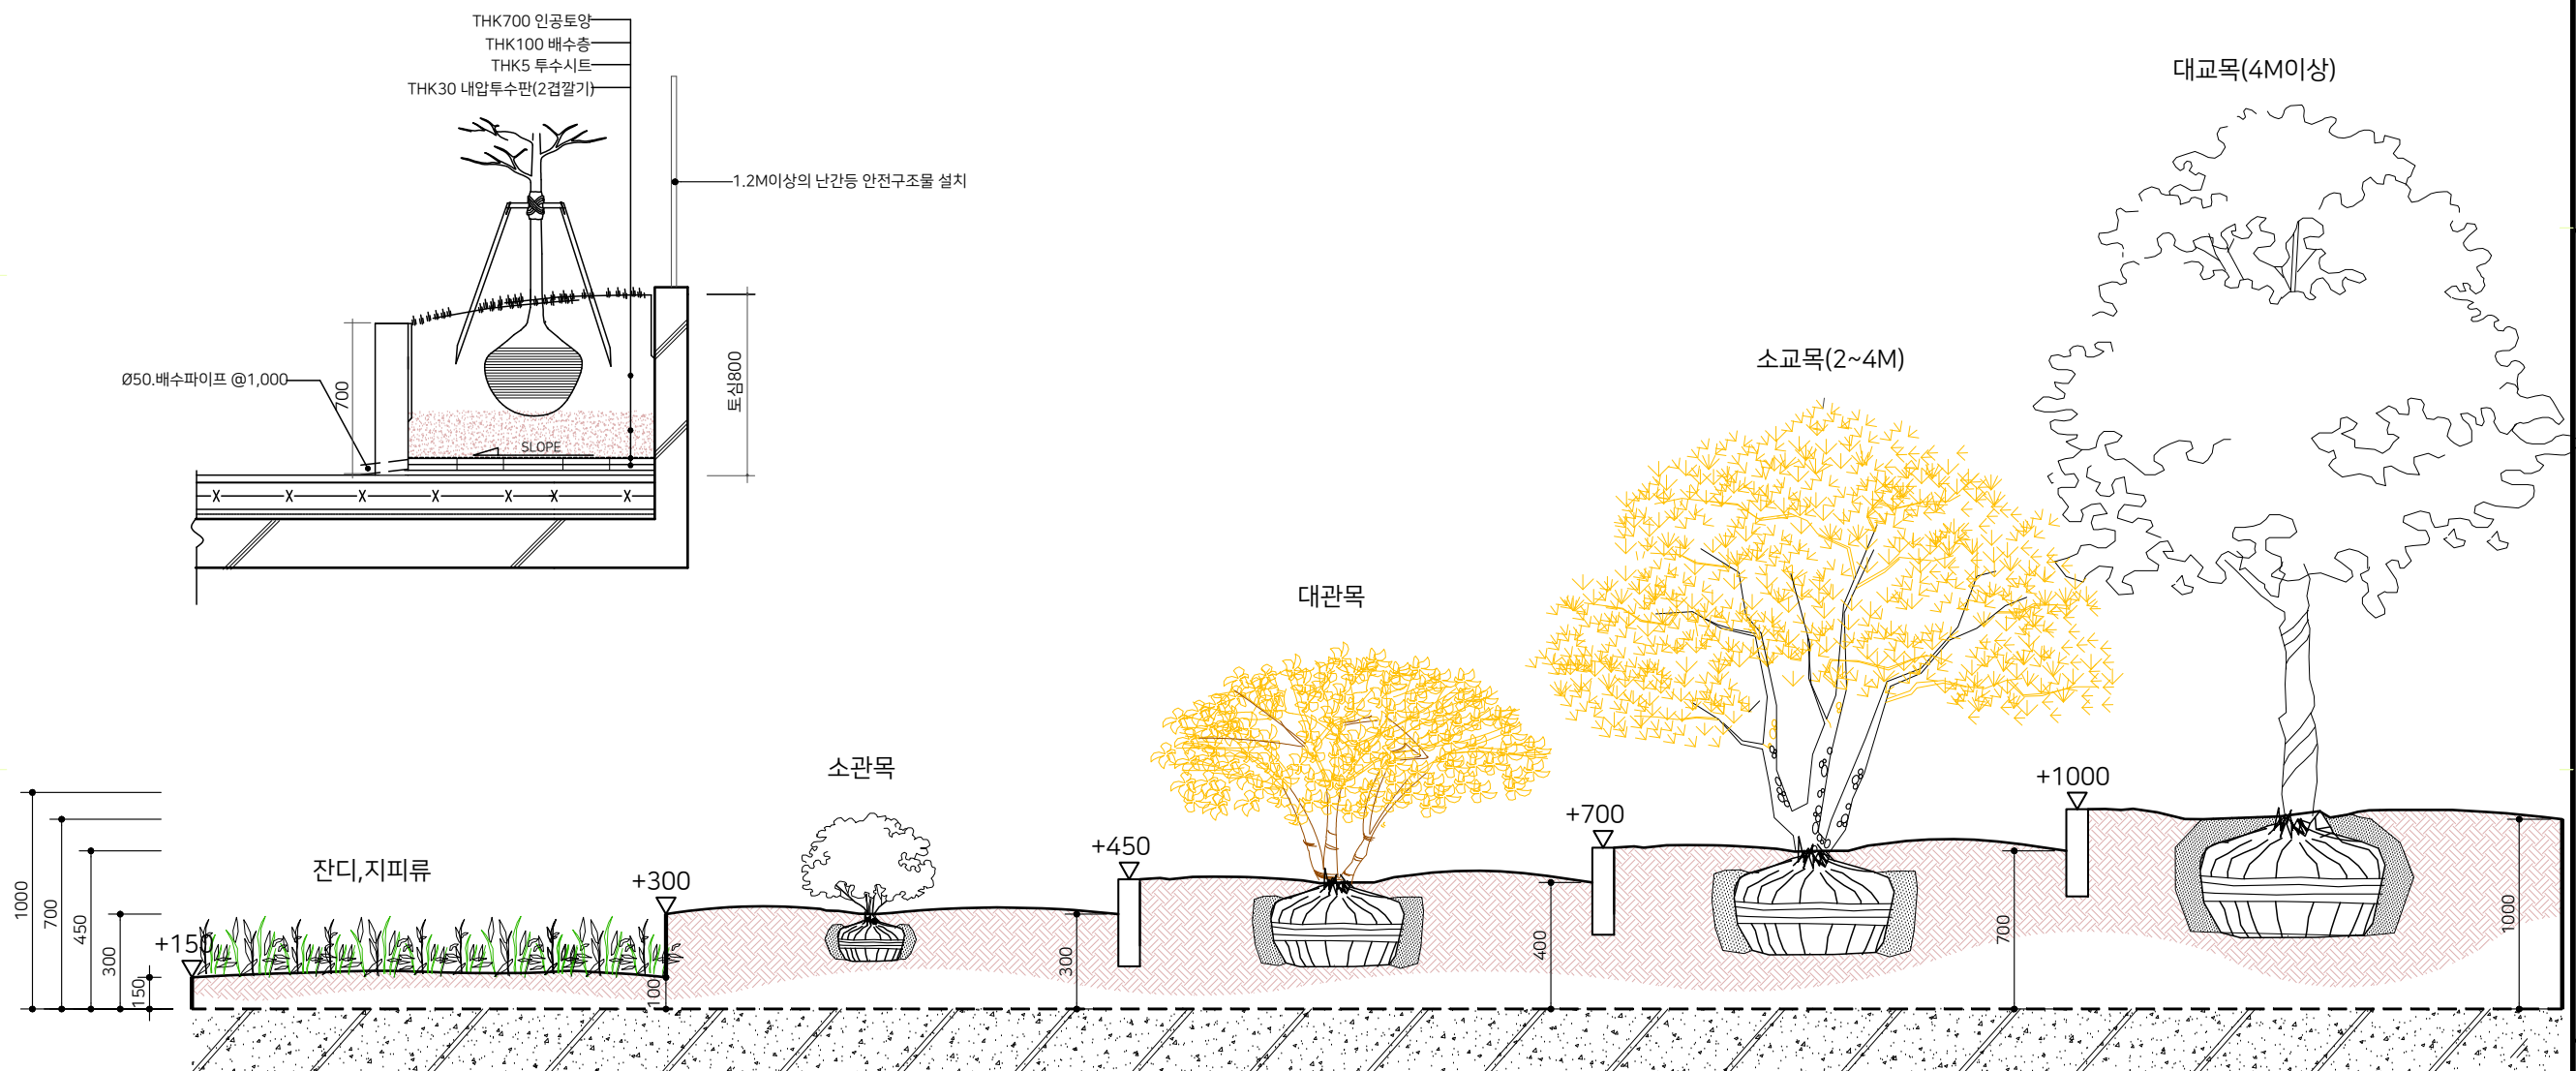

구 분		지 피 류	소 관 목	대 관 목	소 교 목(2~4M)	대 교 목(4M이상)
토 심	자연토양	15cm이상	30cm이상	45cm이상	70cm이상	100cm이상
	인공토양	10cm이상	20cm이상	30cm이상	60cm이상	100cm이상
하 중		45KG/M2	135KG/M2	180KG/M2	315KG/M2	450KG/M2

PROJECT TITLE
화목동 698-14
신축계획안

PROJECT NO.

부산광역시 사하구 하단동 476
TEL . 051 . 791 . 0201
FAX . 051 . 791 . 0203

NOTE

NO.	REVISIONS / ISSUE

ARCHITECTURE DESIGNED BY

STRUCTURE DESIGNED BY

MECHANICAL DESIGNED BY

DRAWN BY

CHECKED BY


APPROVED BY

NAME OF DRAWING
수고별 식재상세


SCALE
A1 SIZE
A3 SIZE
DATE
DRAWING NO.

1 / N
2021
L004

지상1층 면적산정

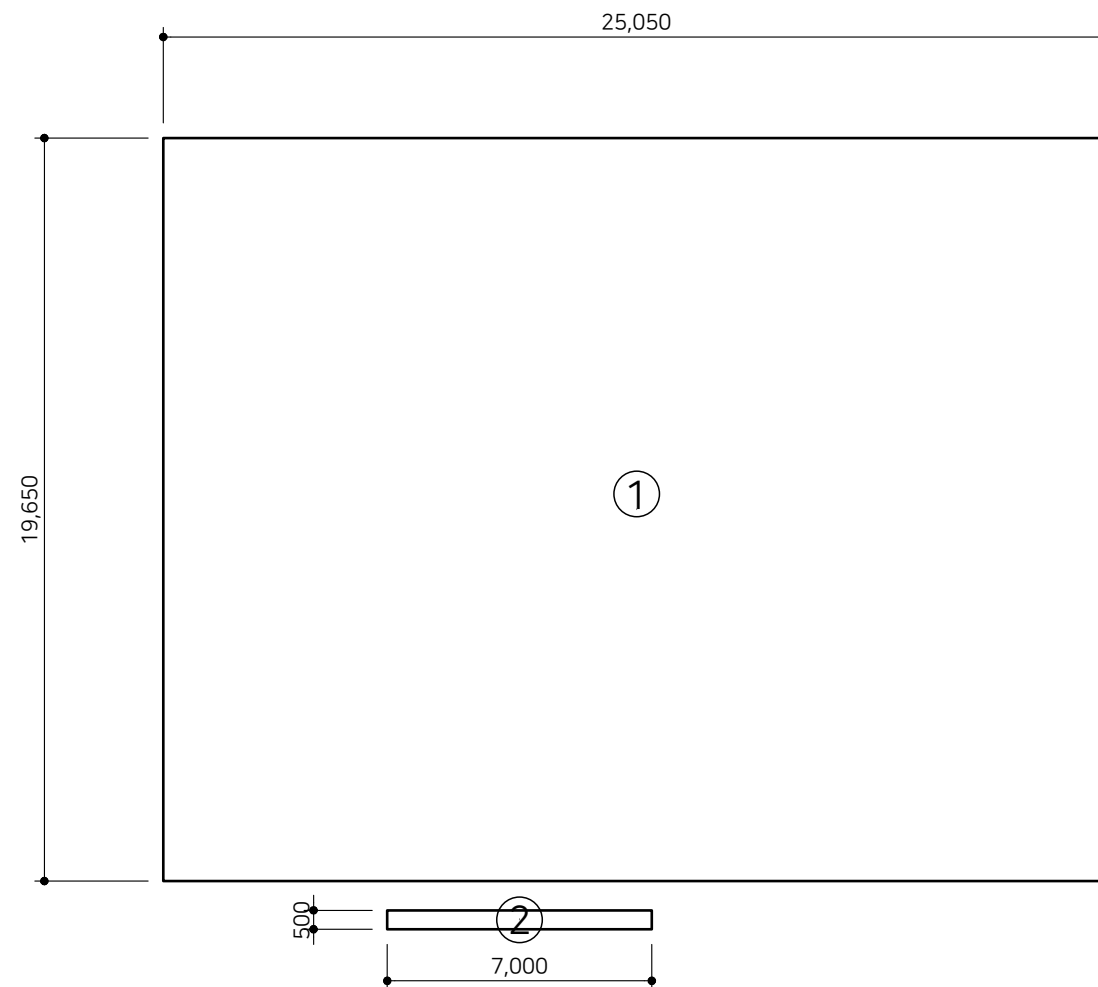

지상2층 면적산정

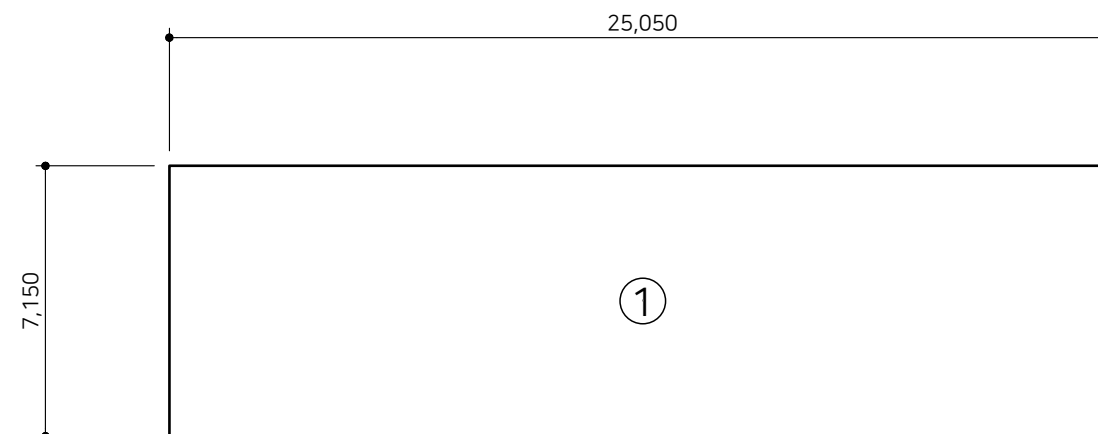[illegible]

NOTE

NO.	REVISIONS / ISSUE	1

ARCHITECTURE DESIGNED BY

STRUCTURE DESIGNED BY

MECHANICAL DESIGNED BY

DRAWN BY _____

CHECKED BY _____

APPROVED BY _____

NAME OF DRAWING

면적산출표-2

SCALE _____
A1 SIZE

A3 SIZE 1 /


DATE 17
2026

DRAWING NO. 2020

A003

부위별 단열 설치 계획표

건물부위 / 위치		두께(mm)	종 류	열전도율(W/mK)
거실외벽	외기에직접 면함	100	그라스울	0.040 이하
최하층 거실바닥	외기에직접 면함	90	임출발보온판 1호	0.25 이하
최상층 거실지붕	외기에직접 면함	180	그라스울	0.040 이하

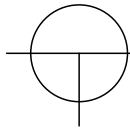

재료마감표

SCALE _ 1/NONE

층 별	실 명	바 닥					결레반이(협의 후 시공)			벽				천 장			
		상세	바 탕	마 감	마 감 두께	비 고	바 탕	마 감	높이	상세	바 탕	마 감	비 고	상세	바 탕	마 감	비 고
1층	수리점	FL-02	T30 시멘트몰탈	에폭시페인트 2회	30	건축주지정	콘크리트 먼처리 or T9.5 석고보드 2PLY or T20 시멘트몰탈	결레받이용 수성페인트	100	WL-01	T9.5 석고보드 2PLY	친환경 수성페인트		CL-01	경량철골천정틀(T-BAR)	T12흡음택스	
	리페어실	FL-01	T27 불임몰탈	T3 데코타일	30	건축주지정	콘크리트 먼처리 or T9.5 석고보드 2PLY or T20 시멘트몰탈	결레받이용 수성페인트	100	WL-01	T9.5 석고보드 2PLY	친환경 수성페인트		CL-01	경량철골천정틀(T-BAR)	T12흡음택스	
	테스트실	FL-01	T27 불임몰탈	T3 데코타일	30	건축주지정	콘크리트 먼처리 or T9.5 석고보드 2PLY or T20 시멘트몰탈	결레받이용 수성페인트	100	WL-01	T9.5 석고보드 2PLY	친환경 수성페인트		CL-01	경량철골천정틀(T-BAR)	T12흡음택스	
	창고	FL-01	T27 불임몰탈	T3 데코타일	30	건축주지정	콘크리트 먼처리 or T9.5 석고보드 2PLY or T20 시멘트몰탈	결레받이용 수성페인트	100	WL-01	T9.5 석고보드 2PLY	친환경 수성페인트		CL-01	경량철골천정틀(T-BAR)	T12흡음택스	
	화장실	FL-04	T60 구배몰탈 T3 무기질게탄성도막방수 액체방수 1층(2차)	T10 포세린타일	80	건축주지정	-	-	-	WL-02	T3 무기질게탄성도막방수 액체방수 1층(2차)	T10 포세린타일	방수 H : 1200	CL-02	경량철골천정틀(CLIP-BAR)	SMC 금속천장재(300X600)	
2층	대표실	FL-01	T27 불임몰탈	T3 데코타일	30	건축주지정	콘크리트 먼처리 or T9.5 석고보드 2PLY or T20 시멘트몰탈	결레받이용 수성페인트	100	WL-01	T9.5 석고보드 2PLY	친환경 수성페인트		CL-01	경량철골천정틀(T-BAR)	T12흡음택스	
	사무실-1	FL-01	T27 불임몰탈	T3 데코타일	30	건축주지정	콘크리트 먼처리 or T9.5 석고보드 2PLY or T20 시멘트몰탈	결레받이용 수성페인트	100	WL-01	T9.5 석고보드 2PLY	친환경 수성페인트		CL-01	경량철골천정틀(T-BAR)	T12흡음택스	
	사무실-2	FL-01	T27 불임몰탈	T3 데코타일	30	건축주지정	콘크리트 먼처리 or T9.5 석고보드 2PLY or T20 시멘트몰탈	결레받이용 수성페인트	100	WL-01	T9.5 석고보드 2PLY	친환경 수성페인트		CL-01	경량철골천정틀(T-BAR)	T12흡음택스	
	탈의실	FL-03	T60 시멘트몰탈 T17 전기바닥판/보온단열재	T3 비닐시트	80		콘크리트 먼처리 or T9.5 석고보드 2PLY or T20 시멘트몰탈	결레받이용 수성페인트	100	WL-01	T9.5 석고보드 2PLY	친환경 수성페인트		CL-01	경량철골천정틀(T-BAR)	T12흡음택스	
	샤워실	FL-04	T60 구배몰탈 T3 무기질게탄성도막방수 액체방수 1층(2차)	T10 포세린타일	80	건축주지정	-	-	-	WL-02	T3 무기질게탄성도막방수 액체방수 1층(2차)	T10 포세린타일	방수 H : 1800	CL-02	경량철골천정틀(CLIP-BAR)	SMC 금속천장재(300X600)	

NOTE

PROJECT TITLE

신진유업
신축공사

PROJECT NO.



부산광역시 사하구 하단동 476
TEL . 051 . 791 . 0201
FAX . 051 . 791 . 0203

NOTE

단열재는 부위별 기준표 및 단면도
준으로 시공한다.

단면도를 참조하여 건적산출.

1.마감재 선택 및 지정색은 추후 2
와 협의 후 시공한다.

2.재료가 분리되는 곳은 재료분리
설치한다.

3.금속부위 도장은 불소수지 도장
칙으로 하며, 부위별 시설별 도장
해서는 감리와 협의 결정.

NO.	REVISIONS / ISSUE	

ARCHITECTURE DESIGNED BY

STRUCTURE DESIGNED BY

MECHANICAL DESIGNED BY

DRAWN BY

CHECKED BY

APPROVED BY

NAME OF DRAWING

재료마감


SCALE

A1 SIZE

A3 SIZE

DATE

DRAWING NO.

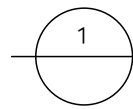

실내재료마감상세도-1

SCALE : 1/NONE

FL		FL-01	데코타일 FIN.
FL		FL-02	에폭시페인트 FIN.
FL		FL-03	비닐시트 FIN.
FL		FL-04	포세린타일 FIN.
WL		WL-01	친환경 수성페인트 FIN.
WL		WL-02	포세린타일 FIN.
CL		CL-1	흡음텍스 FIN.
CL		CL-2	SMC금속천장재 FIN.
ST		ST-F	계단실 바닥_포세린타일 FIN.
ST		ST-C	계단실 천장_친환경수성페인트 FIN.

PROJECT TITLE

PROJECT NO.



부산광역시 사하구 하단동 476
TEL . 051 . 791 . 0201
FAX . 051 . 791 . 0203

NOTE

** 단열기준은 에너지 도면을 기준으로 함

- 마감재 선택 및 지정색은 추후 건축주와 협의후 시공한다.

- 재료가 분리되는 곳은 재료 분리대를 설치한다.

- 금속부위 도장은 불소수지 도장을 원칙으로 하며, 부위 별 시설별 도장과 관련해서는 감리와 협의 결정.

** 실내재료마감상세도를 참조하여 건축

NO.	REVISIONS / ISSUE	DATE

ARCHITECTURE DESIGNED BY

STRUCTURE DESIGNED BY

MECHANICAL DESIGNED BY

DRAWN BY

CHECKED BY

APPROVED BY

NAME OF DRAWING

재료마감상세도-1

SCALE


A1 SIZE

A3 SIZE 1 / 1

DATE

DRAWING NO.

A-1

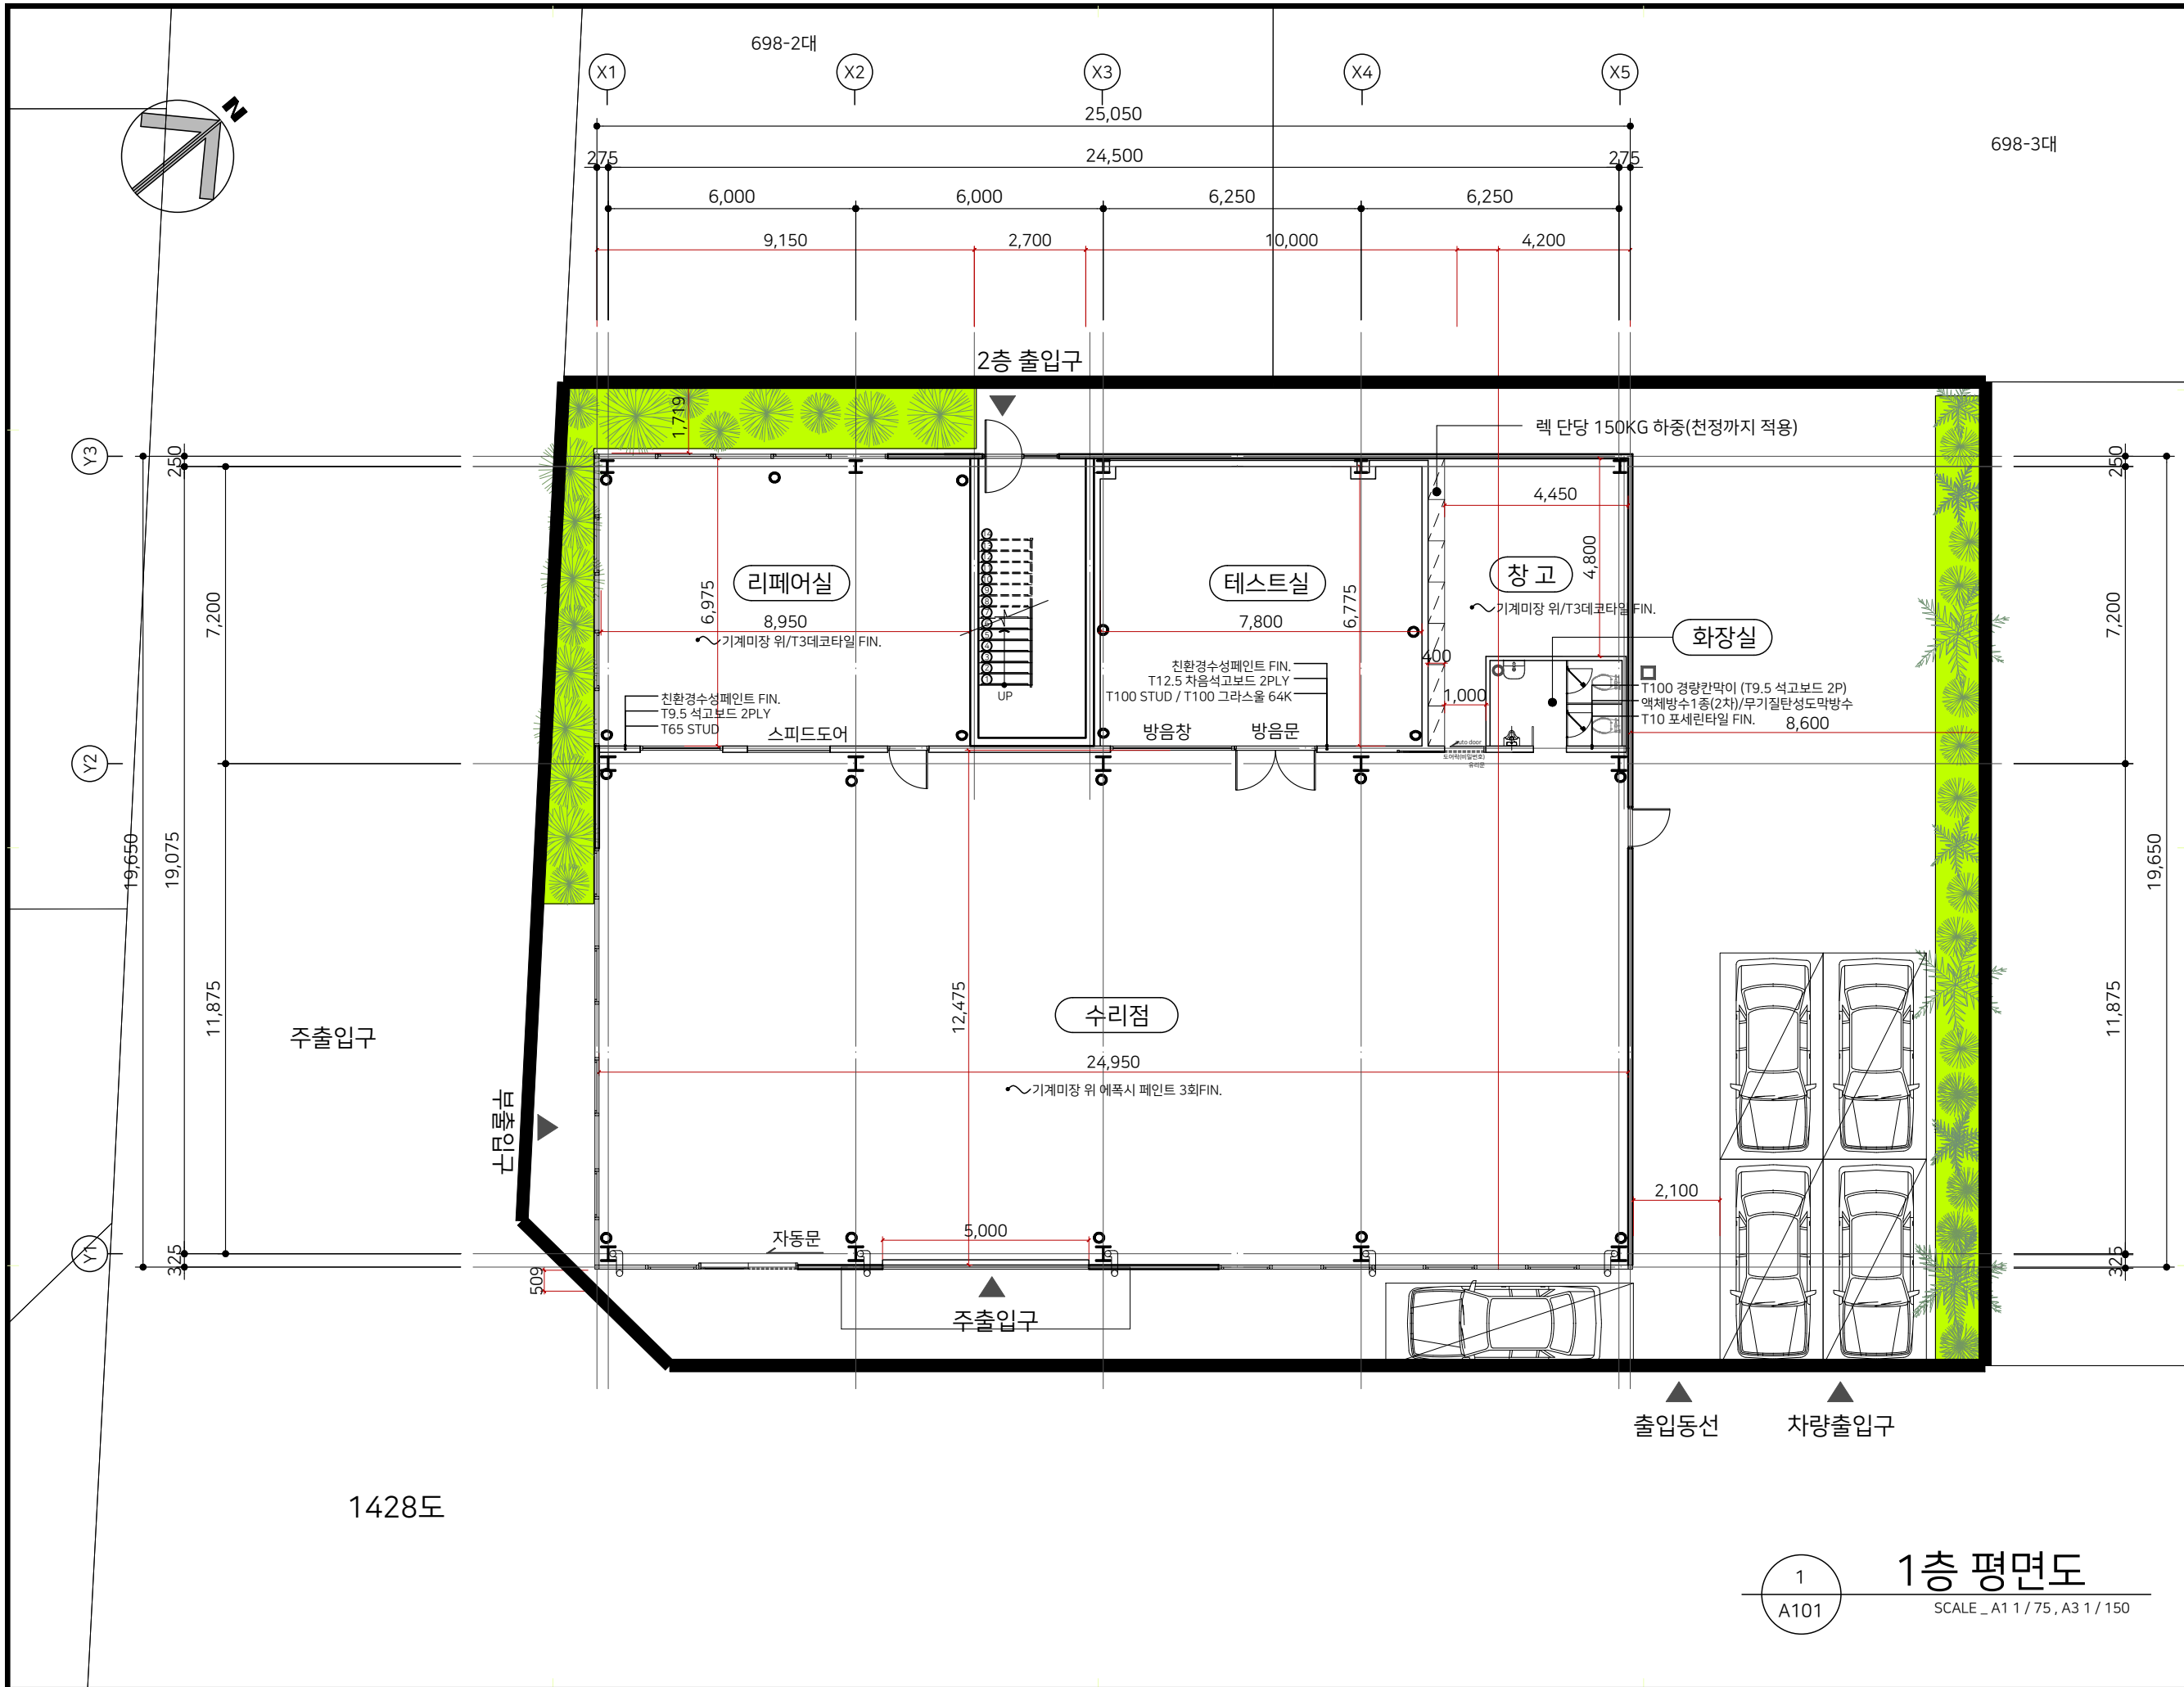

PROJECT TITLE

신진유압
화목동 698-14
신축계획안

PROJECT NO.

지음
건축사
Architects & Interio

부산광역시 사하구 하단동 476
TEL . 051 . 791 . 0201
FAX . 051 . 791 . 0203

NOTE

: 콘센트 및 에어라인

: 수전

: 콘센트

NO.	REVISIONS / ISSUE

ARCHITECTURE DESIGNED BY

STRUCTURE DESIGNED BY

MECHANICAL DESIGNED BY

DRAWN BY

CHECKED BY

APPROVED BY

NAME OF DRAWING

1층 평면도

SCALE

A1 SIZE

A3 SIZE 1 /

DATE 2026


DRAWING NO.

1

A101

1층 평면도

SCALE _ A1 1 / 75 , A3 1 / 150

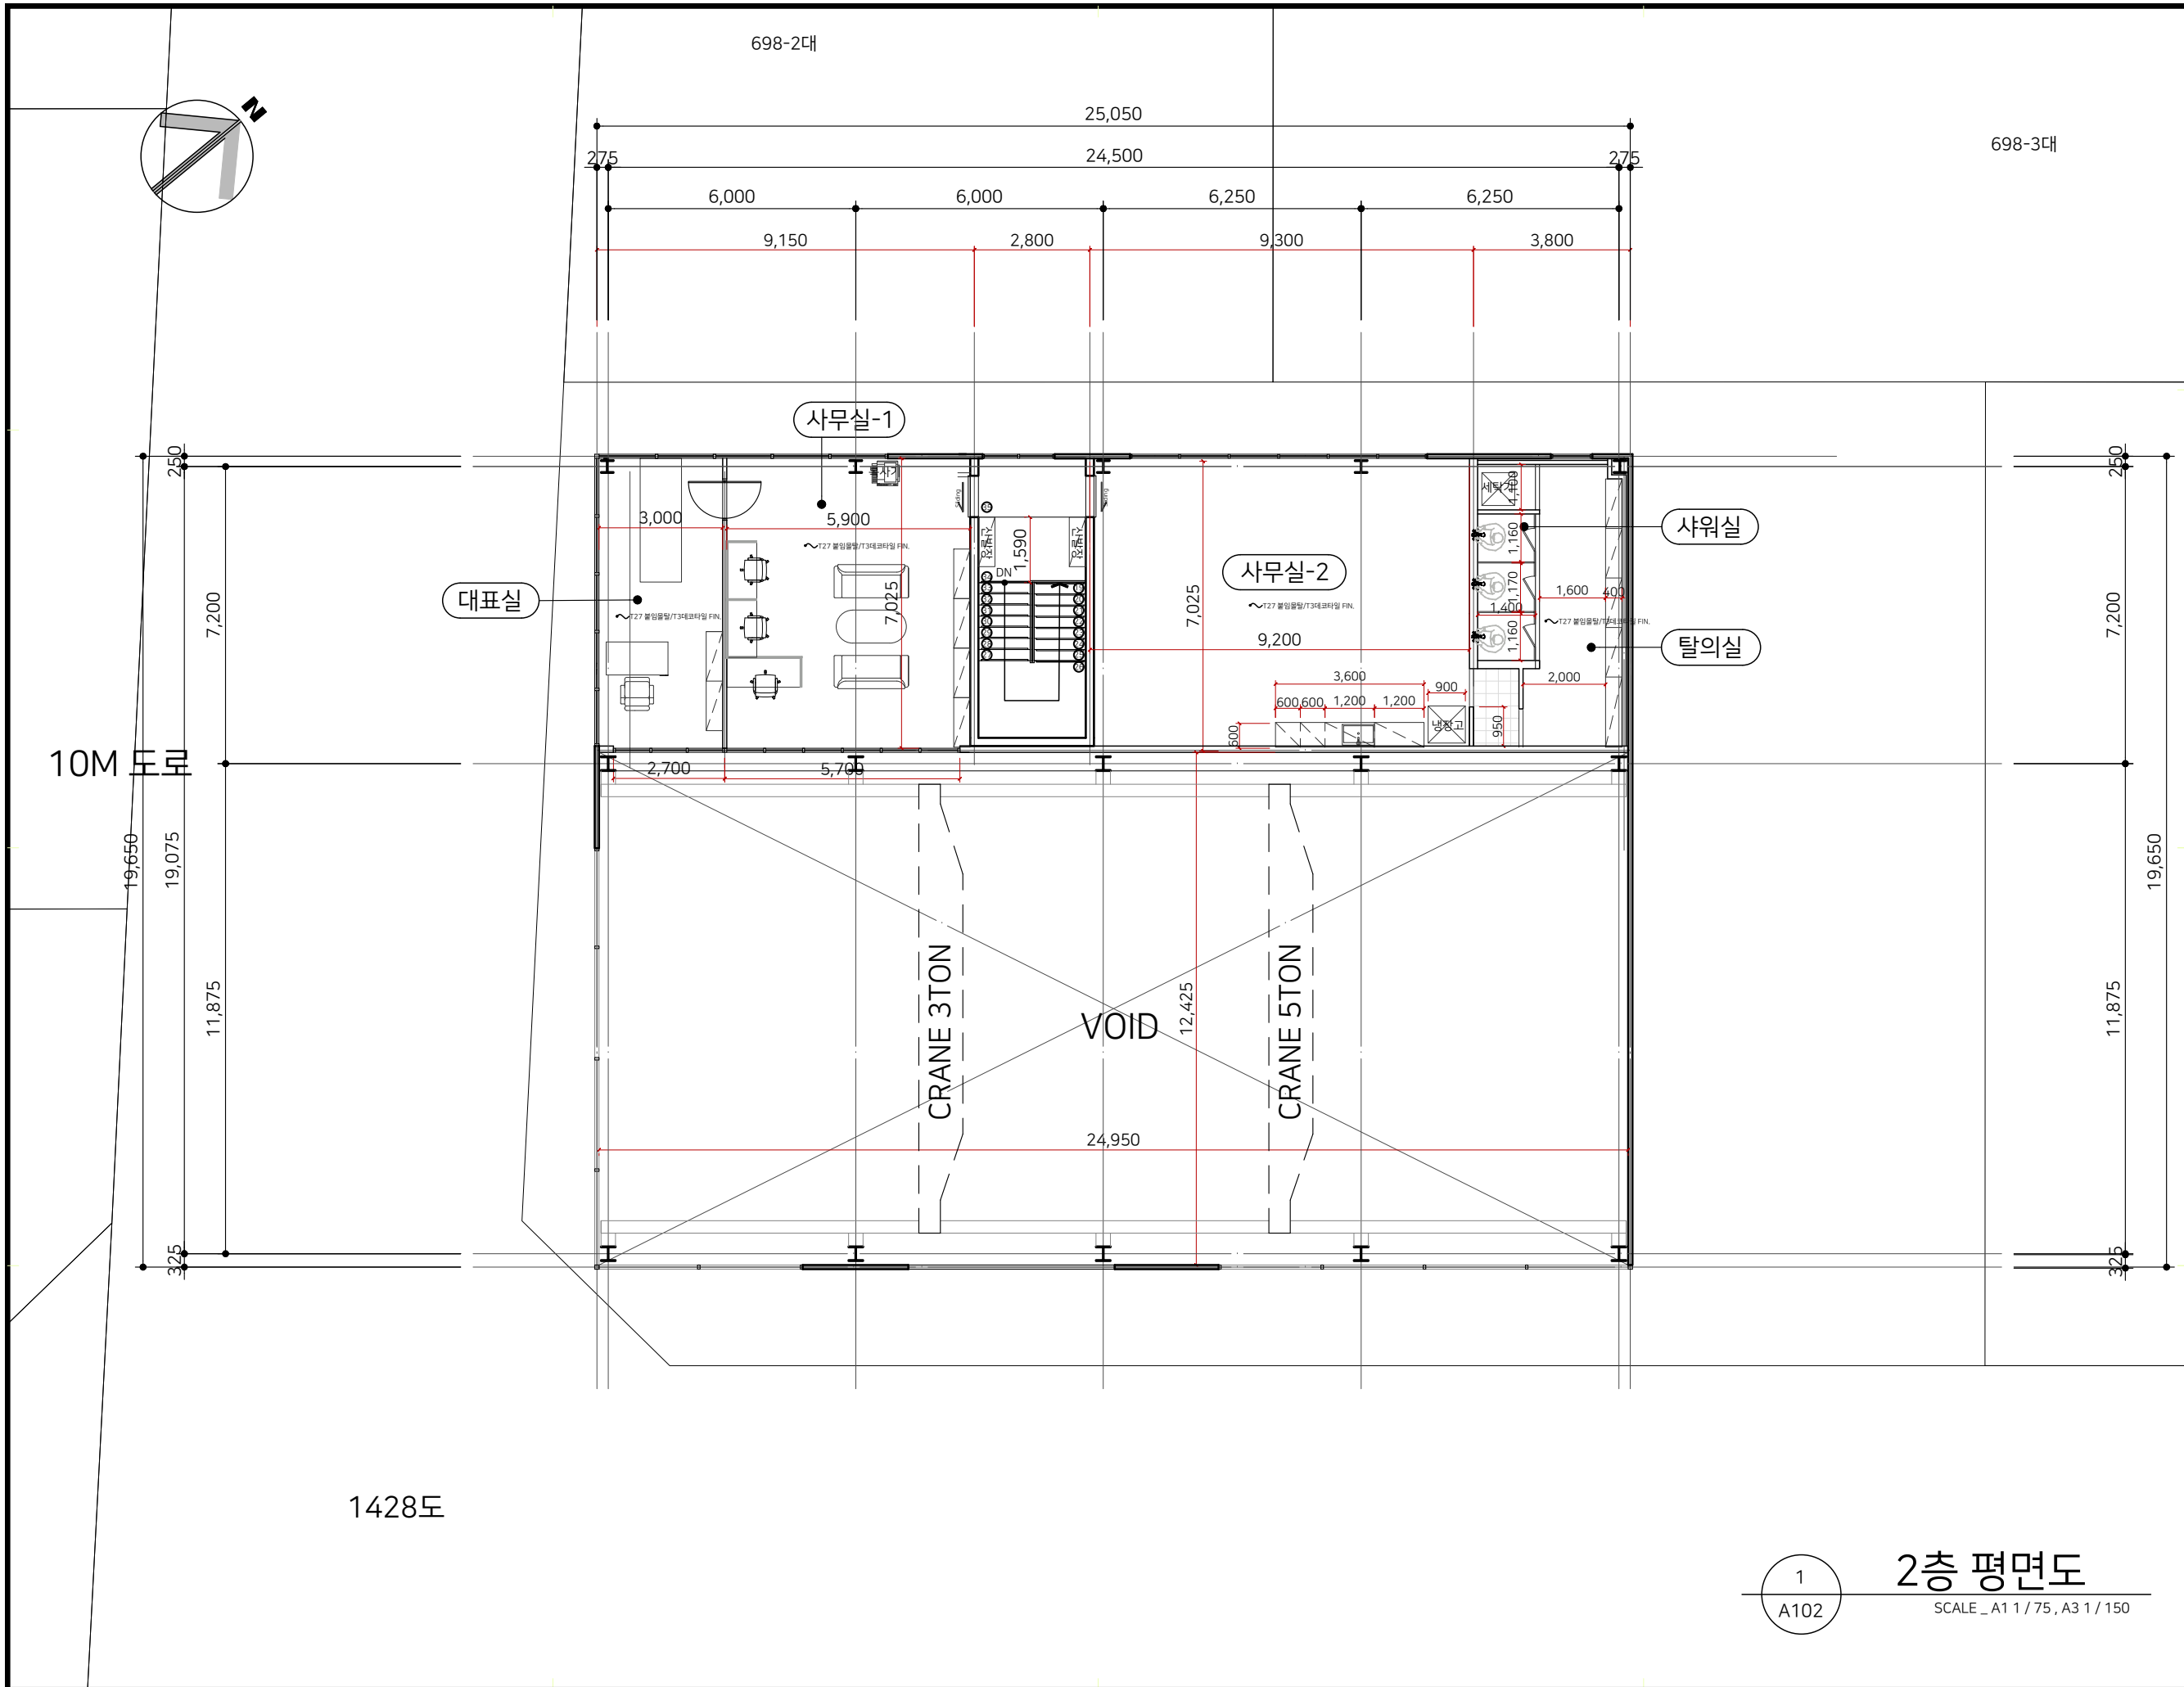

PROJECT TITLE
신진유압
화목동 698-14
신축계획안

PROJECT NO.

지음
건축사사무소
Architects & Interio

부산광역시 사하구 하단동 476
TEL . 051 . 791 . 0201
FAX . 051 . 791 . 0203

NOTE

NO.	REVISIONS / ISSUE

ARCHITECTURE DESIGNED BY

STRUCTURE DESIGNED BY

MECHANICAL DESIGNED BY

DRAWN BY

CHECKED BY

APPROVED BY

NAME OF DRAWING

2층 평면도


SCALE

A1 SIZE

A3 SIZE 1 /

DATE 2026

DRAWING NO.

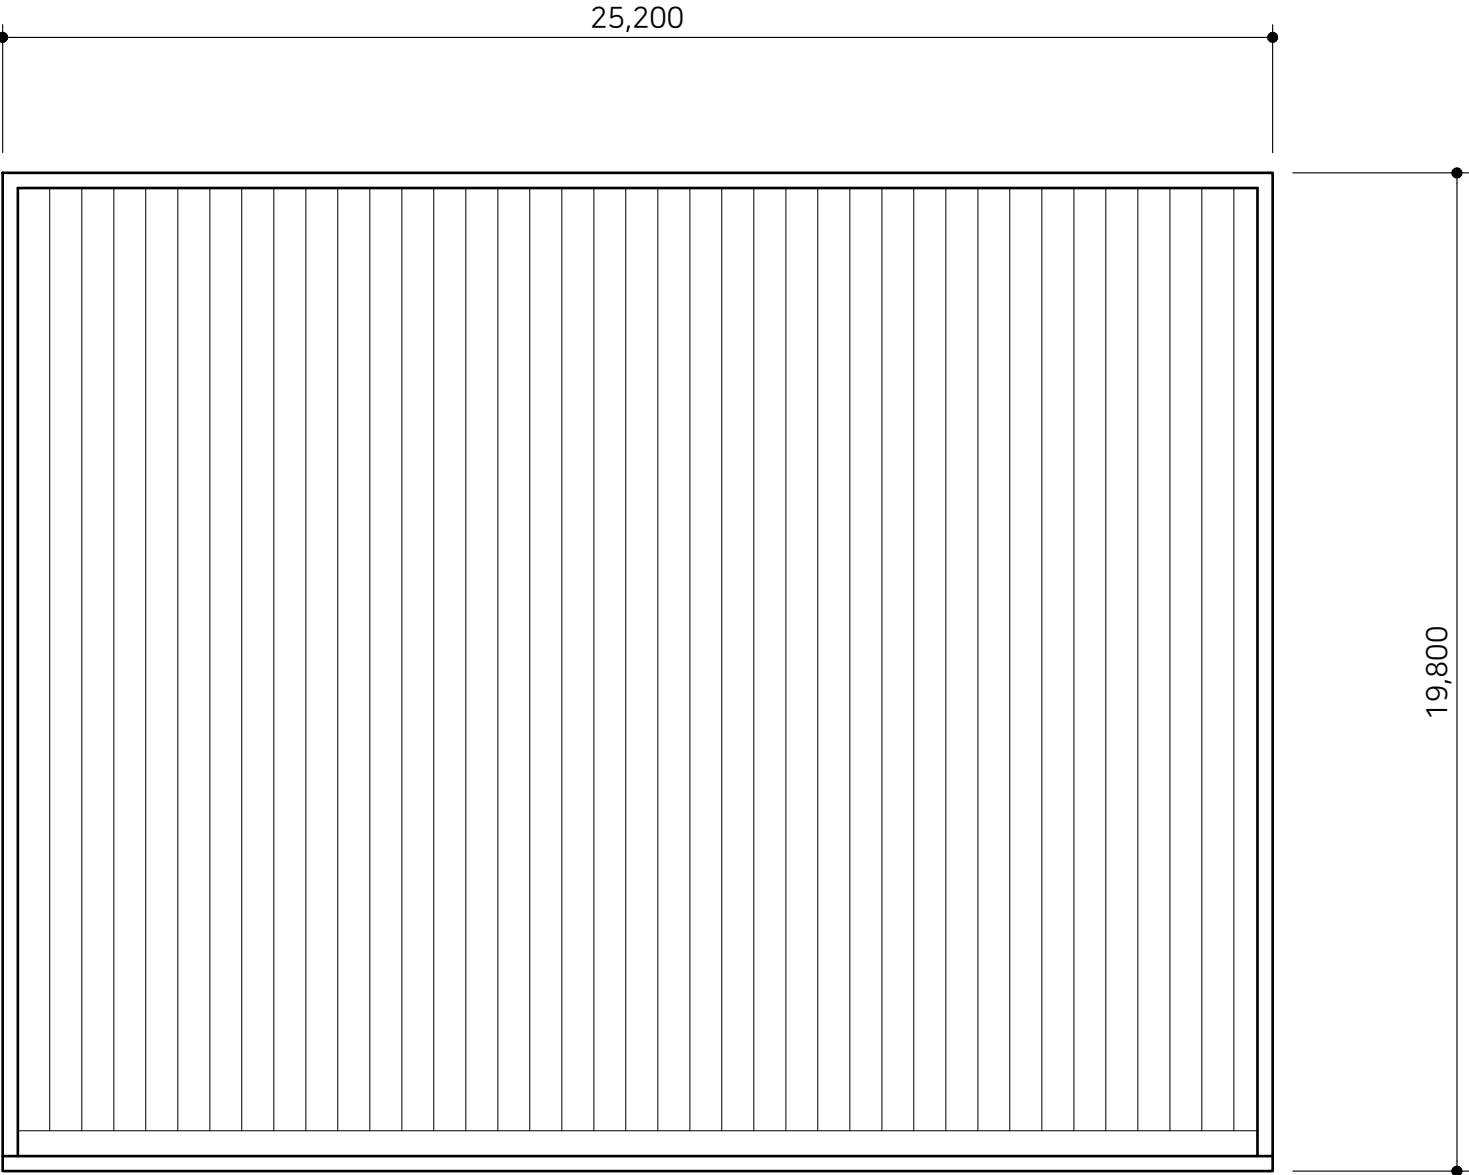

1
A103

지붕평면도

SCALE _ A1 1 / 75 , A3 1 / 150

PROJECT TITLE

신진유압
화목동 698-14
신축계획안

PROJECT NO.



부산광역시 사하구 하단동 476
TEL . 051 . 791 . 0201
FAX . 051 . 791 . 0203

NOTE

NO.	REVISIONS / ISSUE	

ARCHITECTURE DESIGNED BY

STRUCTURE DESIGNED BY

MECHANICAL DESIGNED BY

DRAWN BY

CHECKED BY

APPROVED BY

NAME OF DRAWING

지붕평면도

SCALE

A1 SIZE



A3 SIZE

DATE

DRAWING NO.

1 /

2026

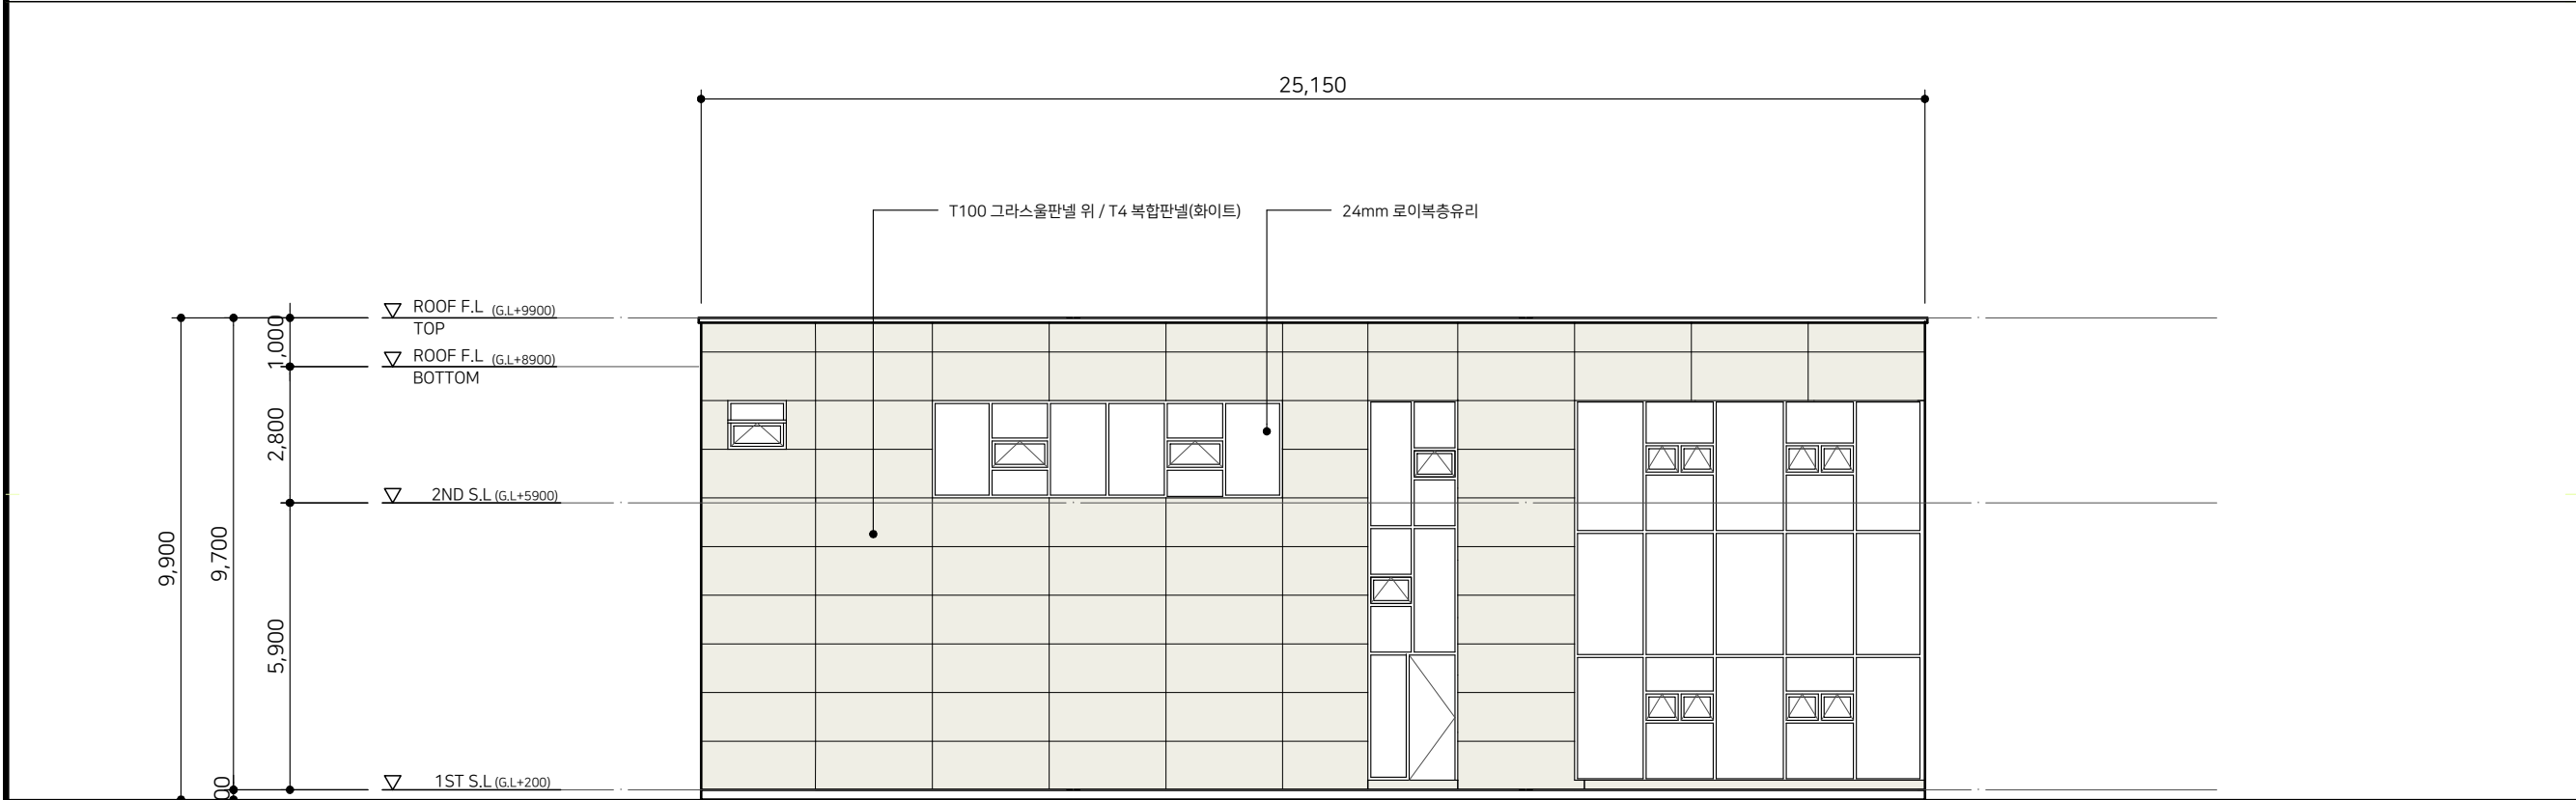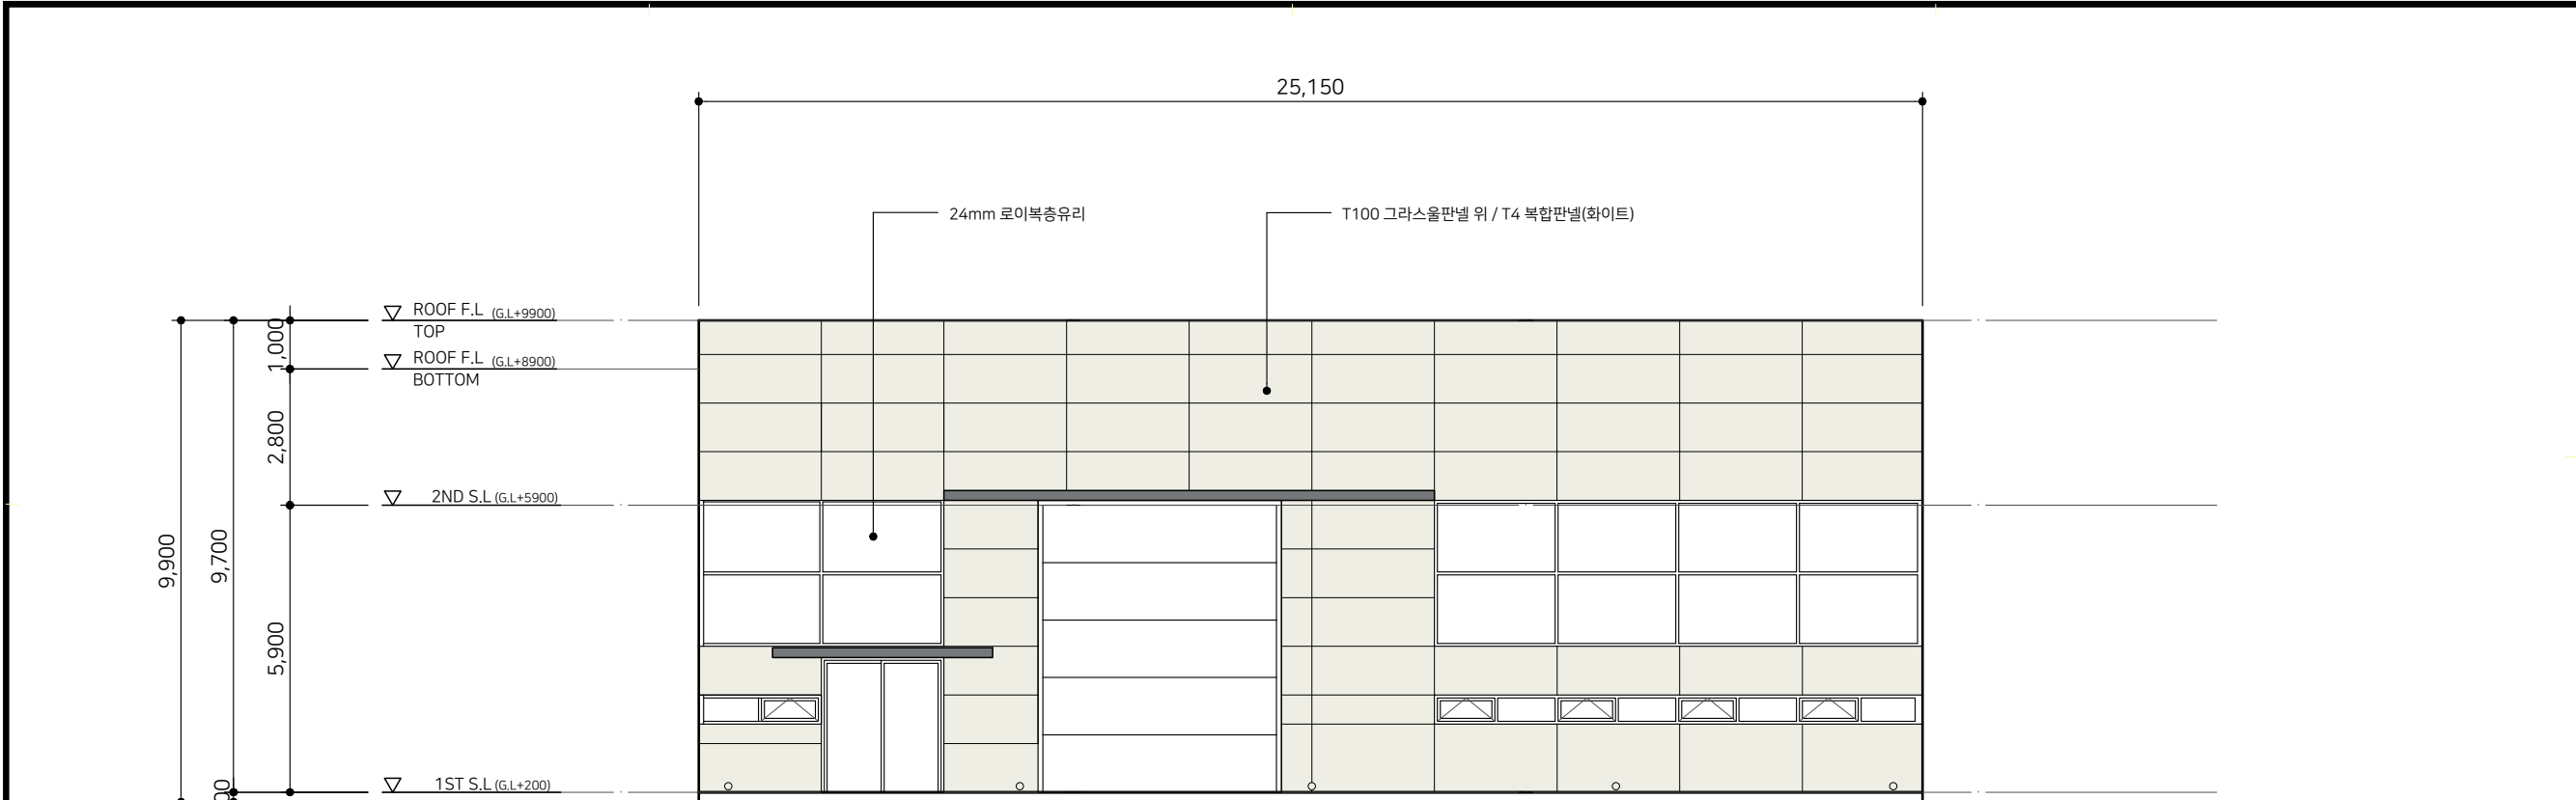

1
A201

정면도 / 배면도

SCALE _ A1 1 / 75 , A3 1 / 150

PROJECT TITLE
신진유압
화목동 698-14
신축계획안

PROJECT NO.


지음
건축사사무소
Architects & Interio

부산광역시 사하구 하단동 476
TEL . 051 . 791 . 0201
FAX . 051 . 791 . 0203

NOTE

NO.	REVISIONS / ISSUE	

ARCHITECTURE DESIGNED BY

STRUCTURE DESIGNED BY

MECHANICAL DESIGNED BY

DRAWN BY



CHECKED BY

APPROVED BY

NAME OF DRAWING

정면도 / 배면도

SCALE
A1 SIZE
A3 SIZE 1 /
DATE 2026
DRAWING NO.

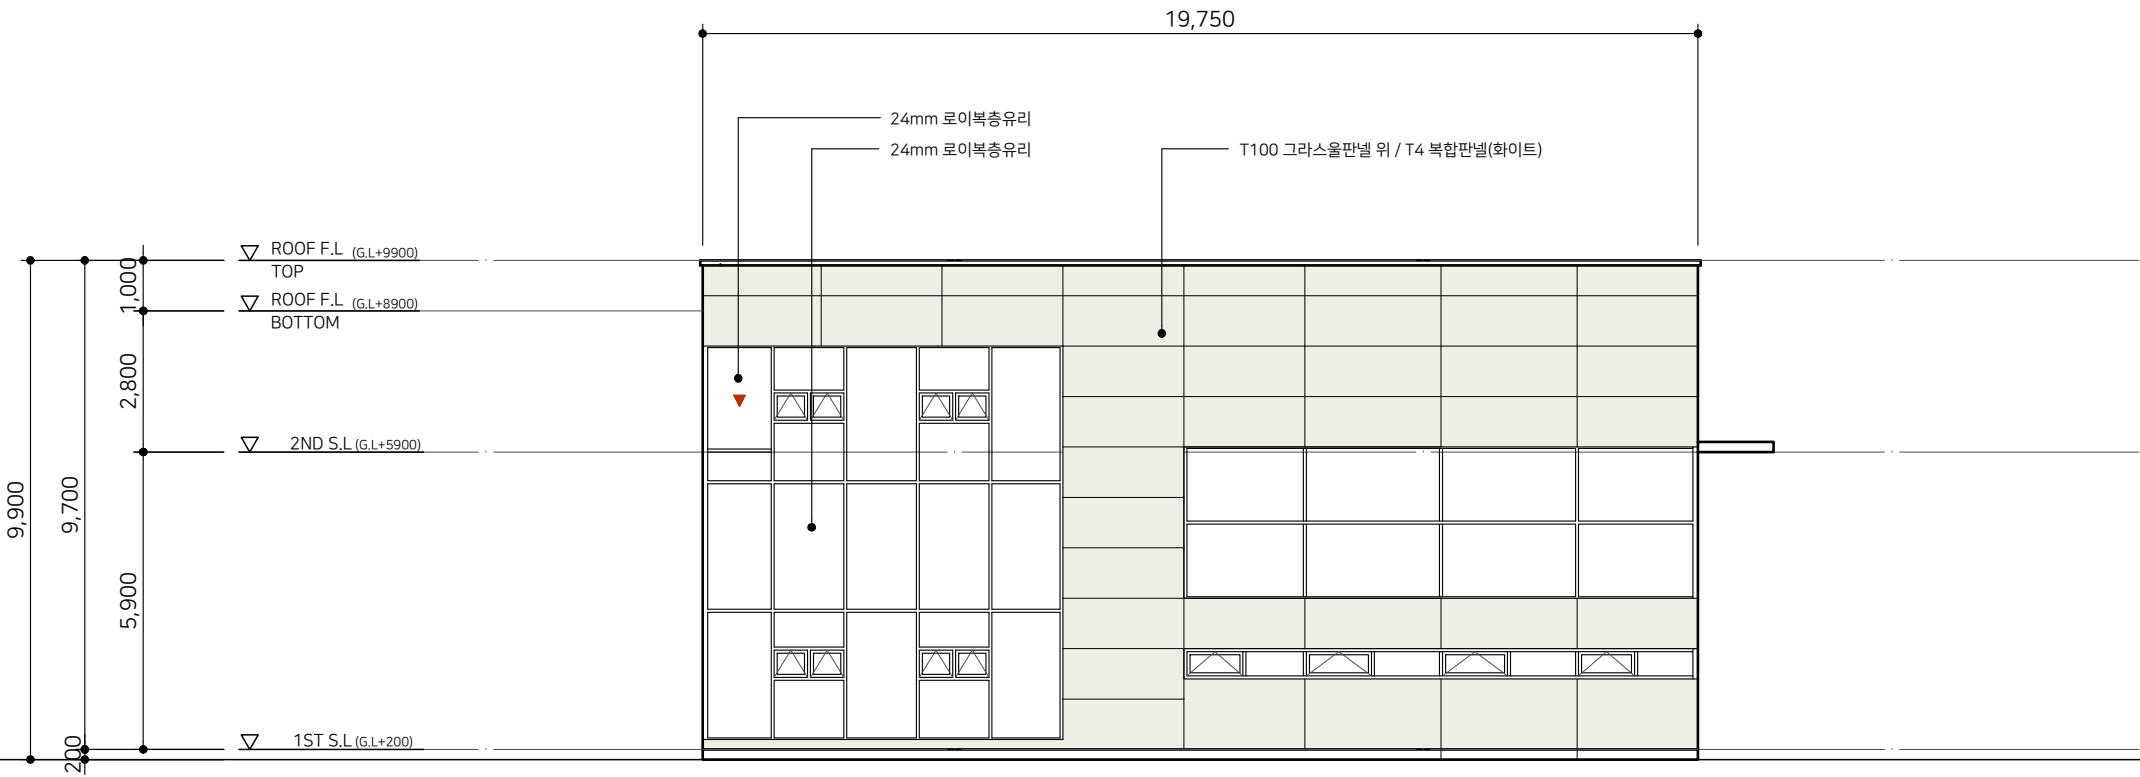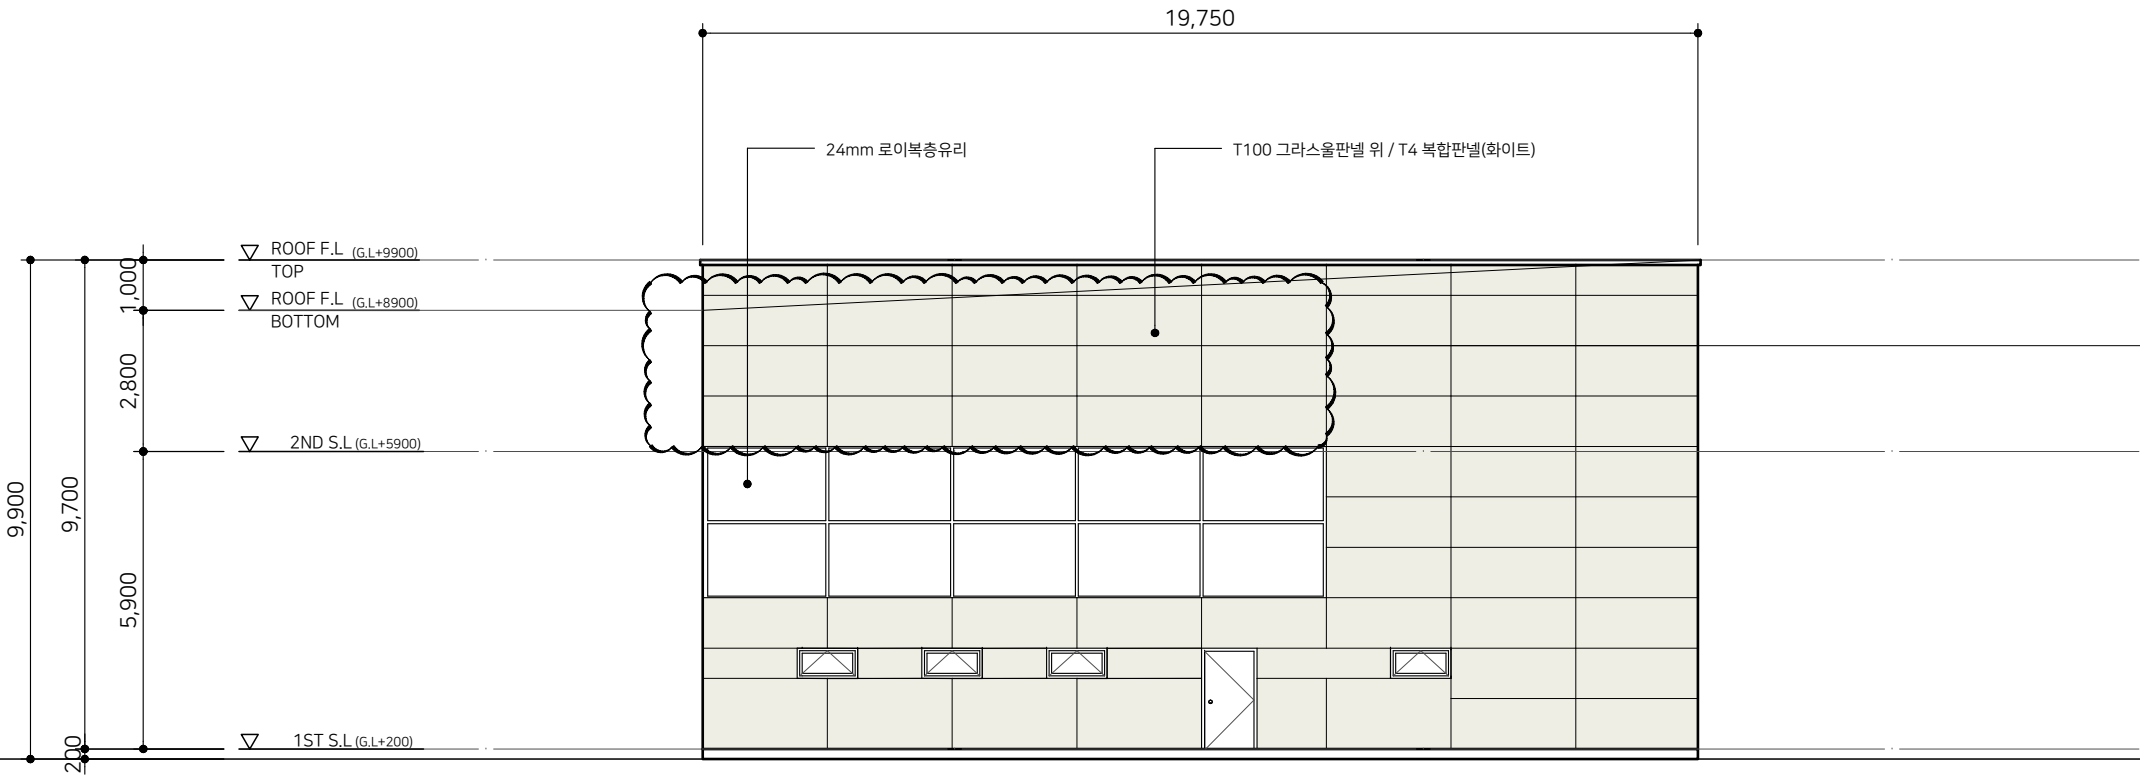

1
A202

좌측면도/우측면도

SCALE _ A1 1 / 75 , A3 1 / 150

PROJECT TITLE
신진유압
화목동 698-14
신축계획안

PROJECT NO.


부산광역시 사하구 하단동 476
TEL . 051 . 791 . 0201
FAX . 051 . 791 . 0203

NOTE

NO.	REVISIONS / ISSUE	

ARCHITECTURE DESIGNED BY

STRUCTURE DESIGNED BY

MECHANICAL DESIGNED BY

DRAWN BY

CHECKED BY

APPROVED BY

NAME OF DRAWING

좌측면도/우측면도

SCALE	
A1 SIZE	
A3 SIZE	1 /
DATE	2026
DRAWING NO.	

PROJECT TITLE
신진유압
화목동 698-14
신축계획안

PROJECT NO.



부산광역시 사하구 하단동 476
TEL . 051 . 791 . 0201
FAX . 051 . 791 . 0203

NOTE

NO.	REVISIONS / ISSUE	

ARCHITECTURE DESIGNED BY

STRUCTURE DESIGNED BY

MECHANICAL DESIGNED BY

DRAWN BY


CHECKED BY

APPROVED BY


NAME OF DRAWING

종단면도-1
종단면도-2


SCALE
A1 SIZE
A3 SIZE 1 /
DATE 2026
DRAWING NO.

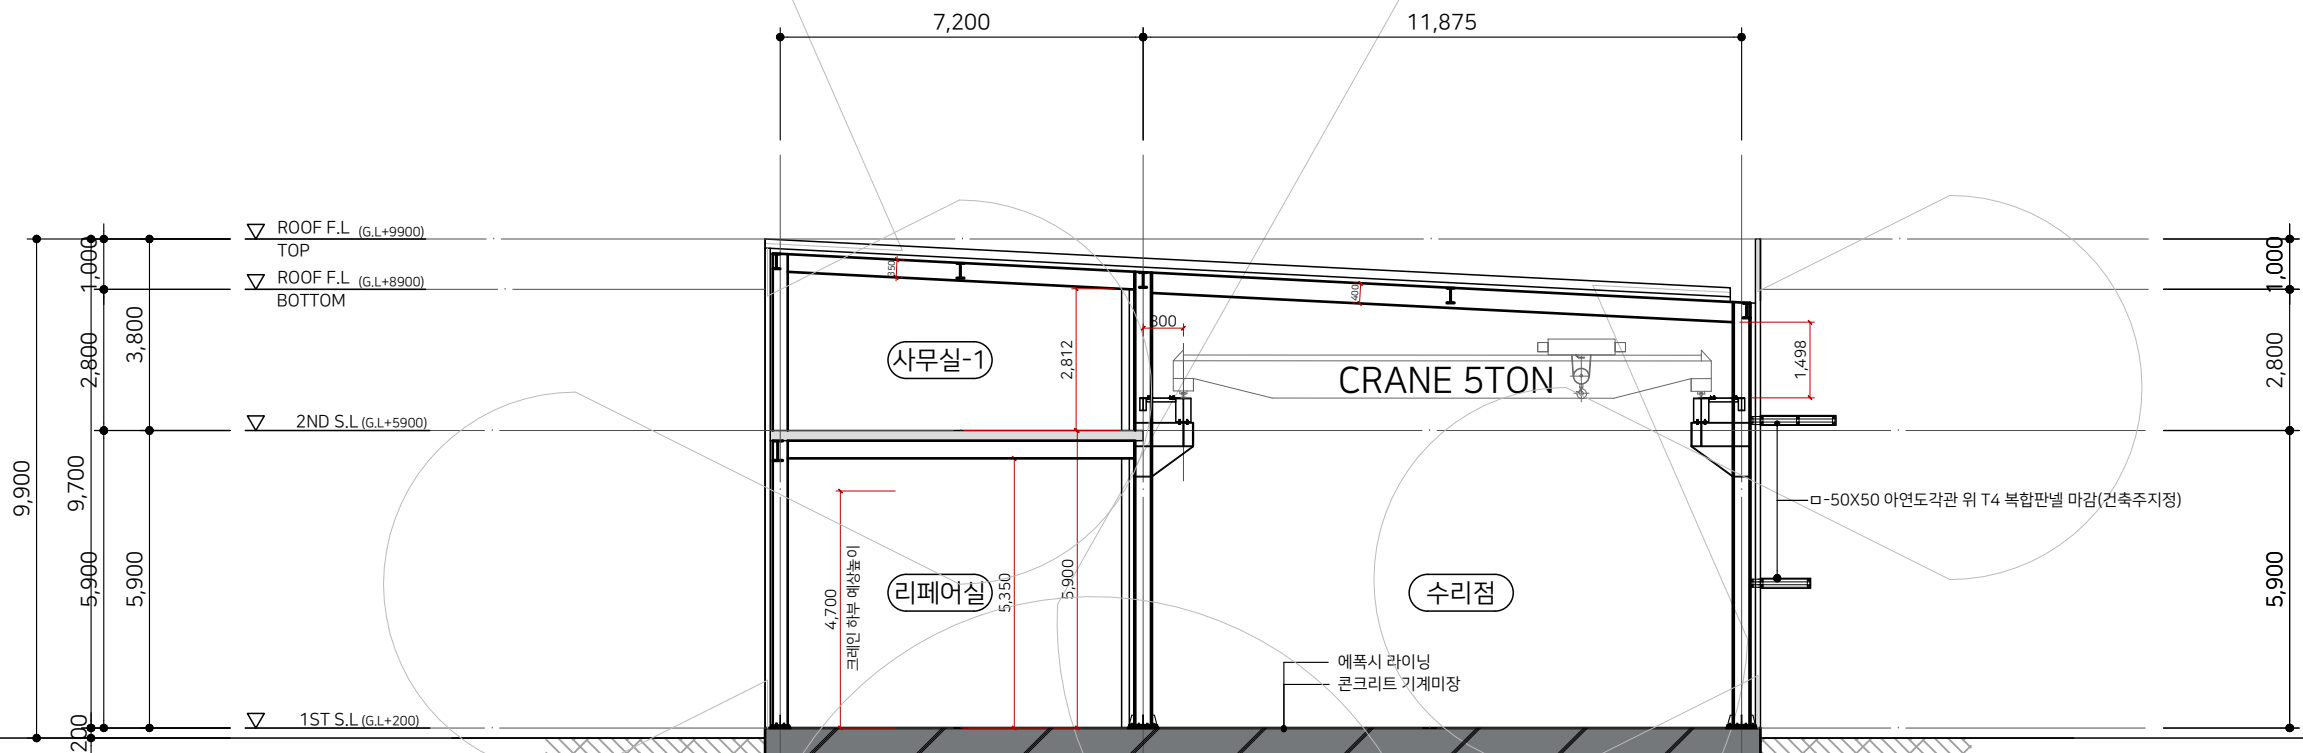

1
A301
종단면도-1
SCALE _ A1 1 / 75 , A3 1 / 150

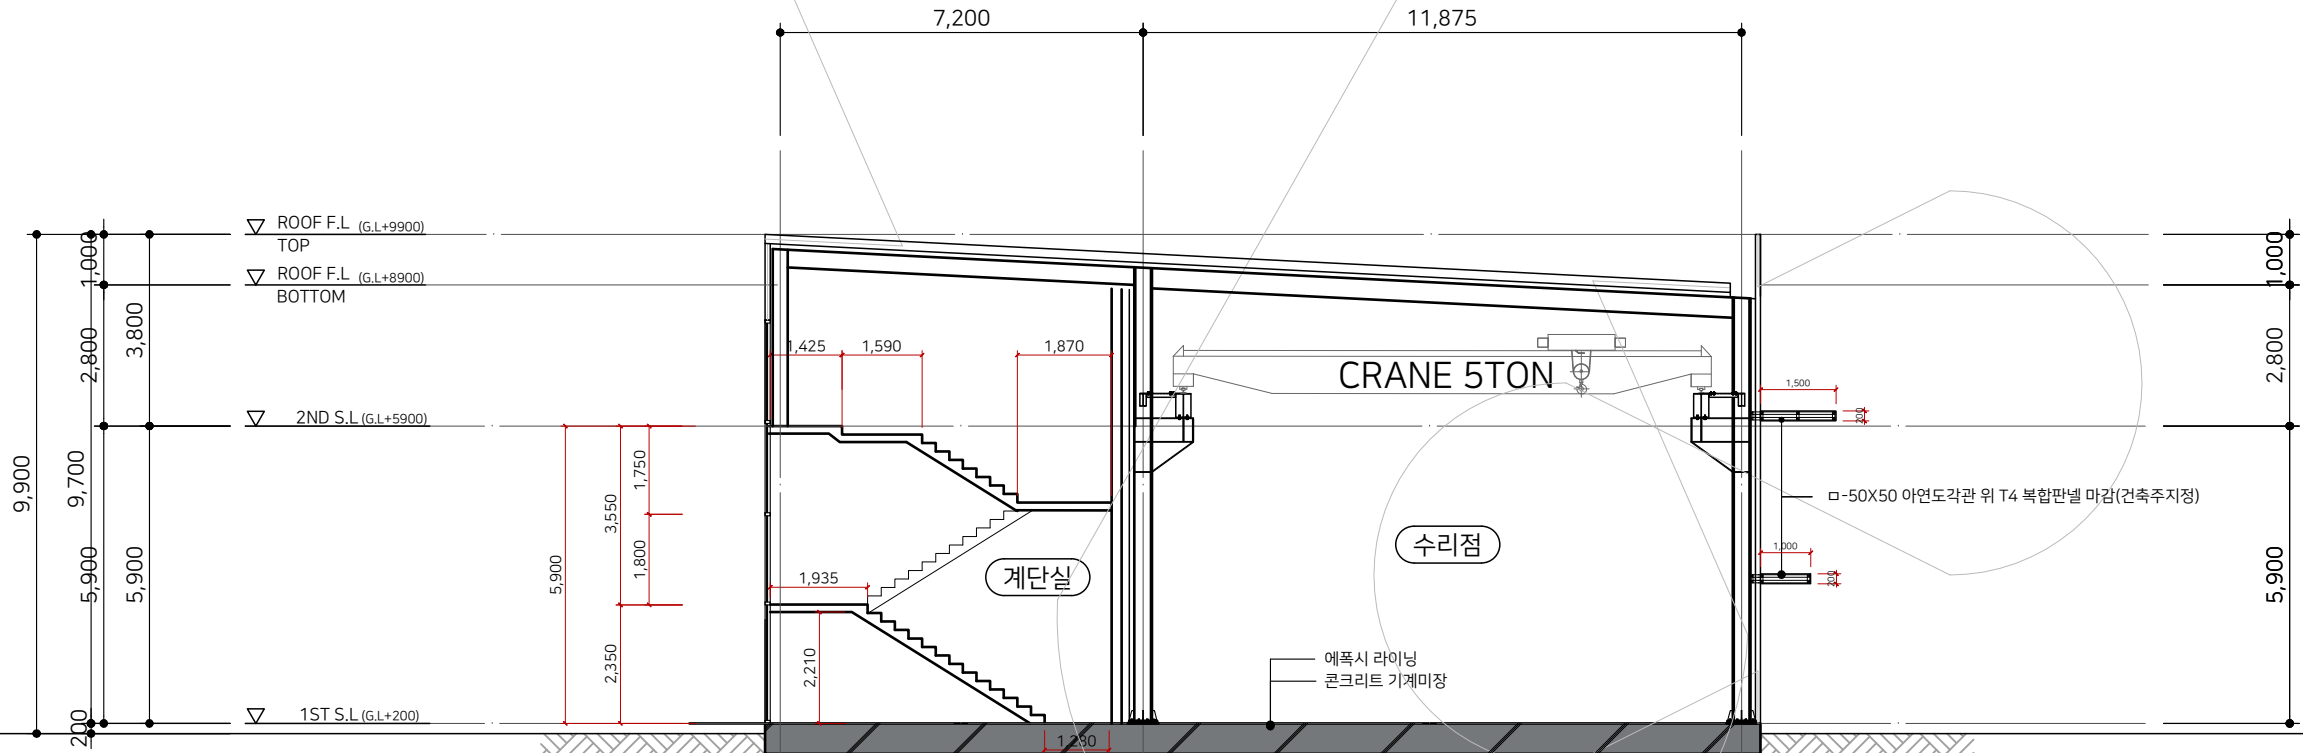

1
A301
종단면도-2
SCALE _ A1 1 / 75 , A3 1 / 150

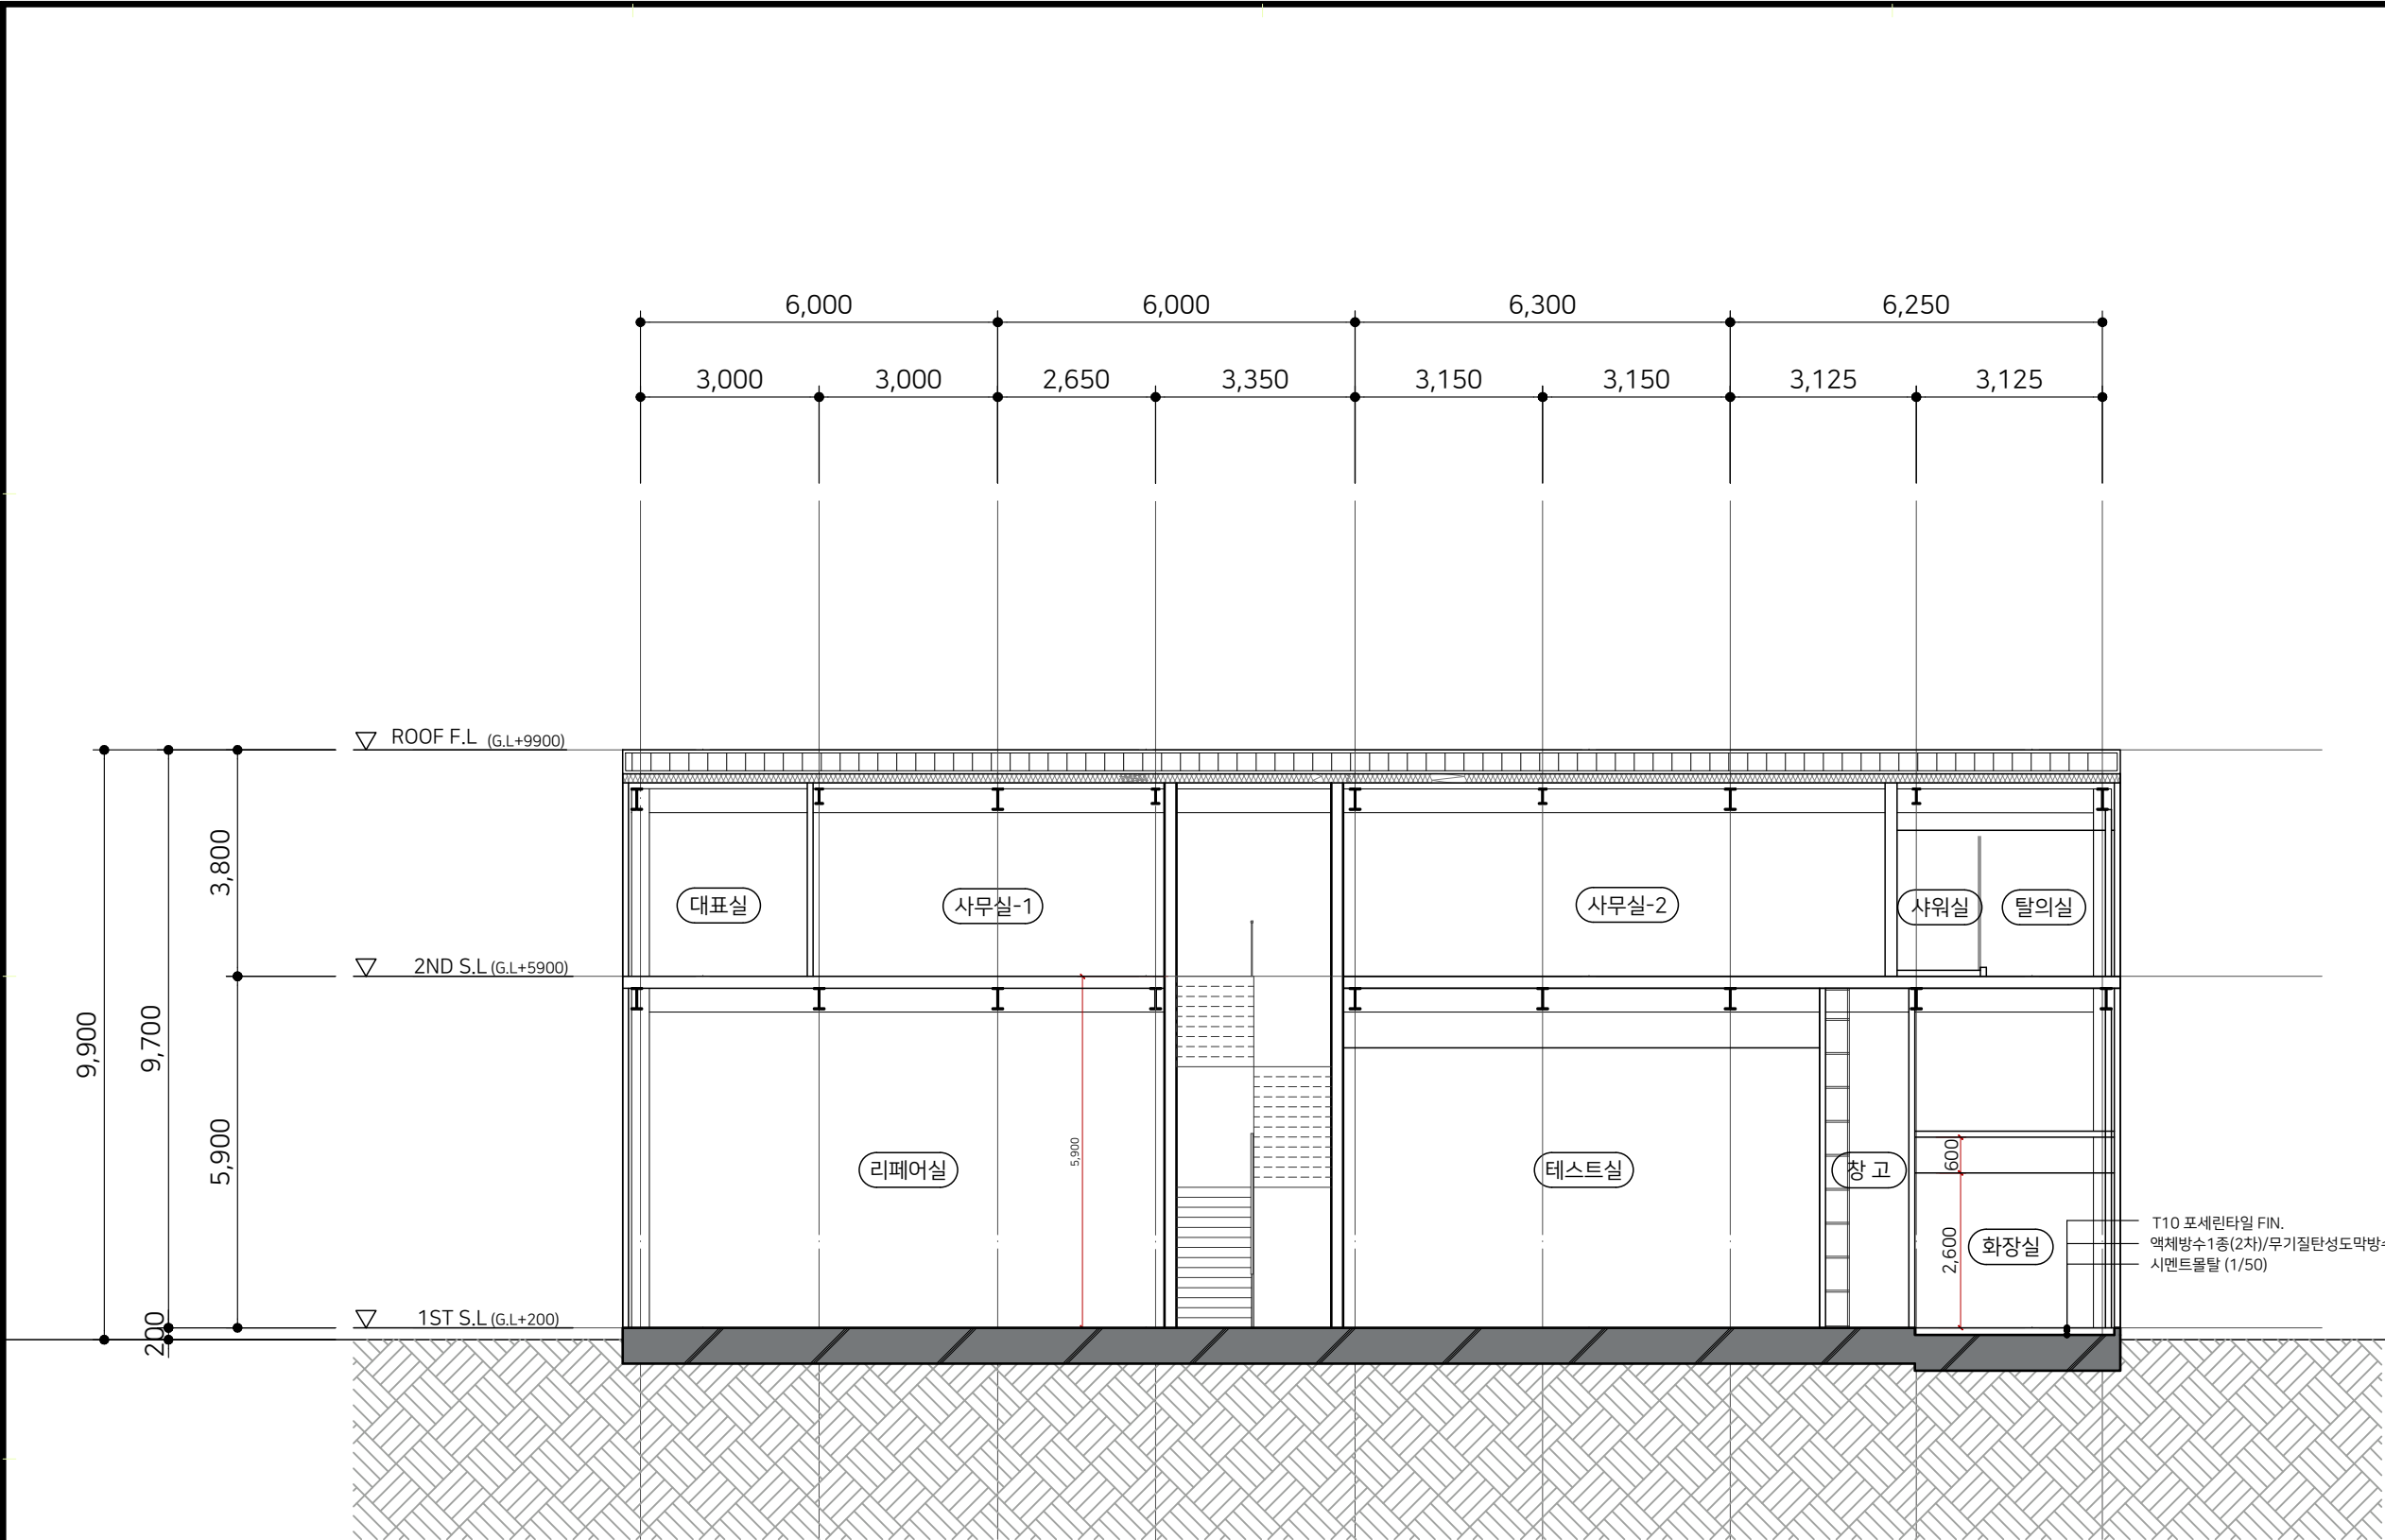

PROJECT TITLE
신진유압
화목동 698-14
신축계획안

PROJECT NO.



부산광역시 사하구 하단동 476
TEL . 051 . 791 . 0201
FAX . 051 . 791 . 0203

NOTE

NO.	REVISIONS / ISSUE

ARCHITECTURE DESIGNED BY

STRUCTURE DESIGNED BY

MECHANICAL DESIGNED BY

DRAWN BY

CHECKED BY

APPROVED BY

NAME OF DRAWING


횡단면도

SCALE
A1 SIZE
A3 SIZE 1 /
DATE 2026
DRAWING NO.

1
A302

횡단면도

SCALE _ A1 1 / 60. , A3 1 / 120

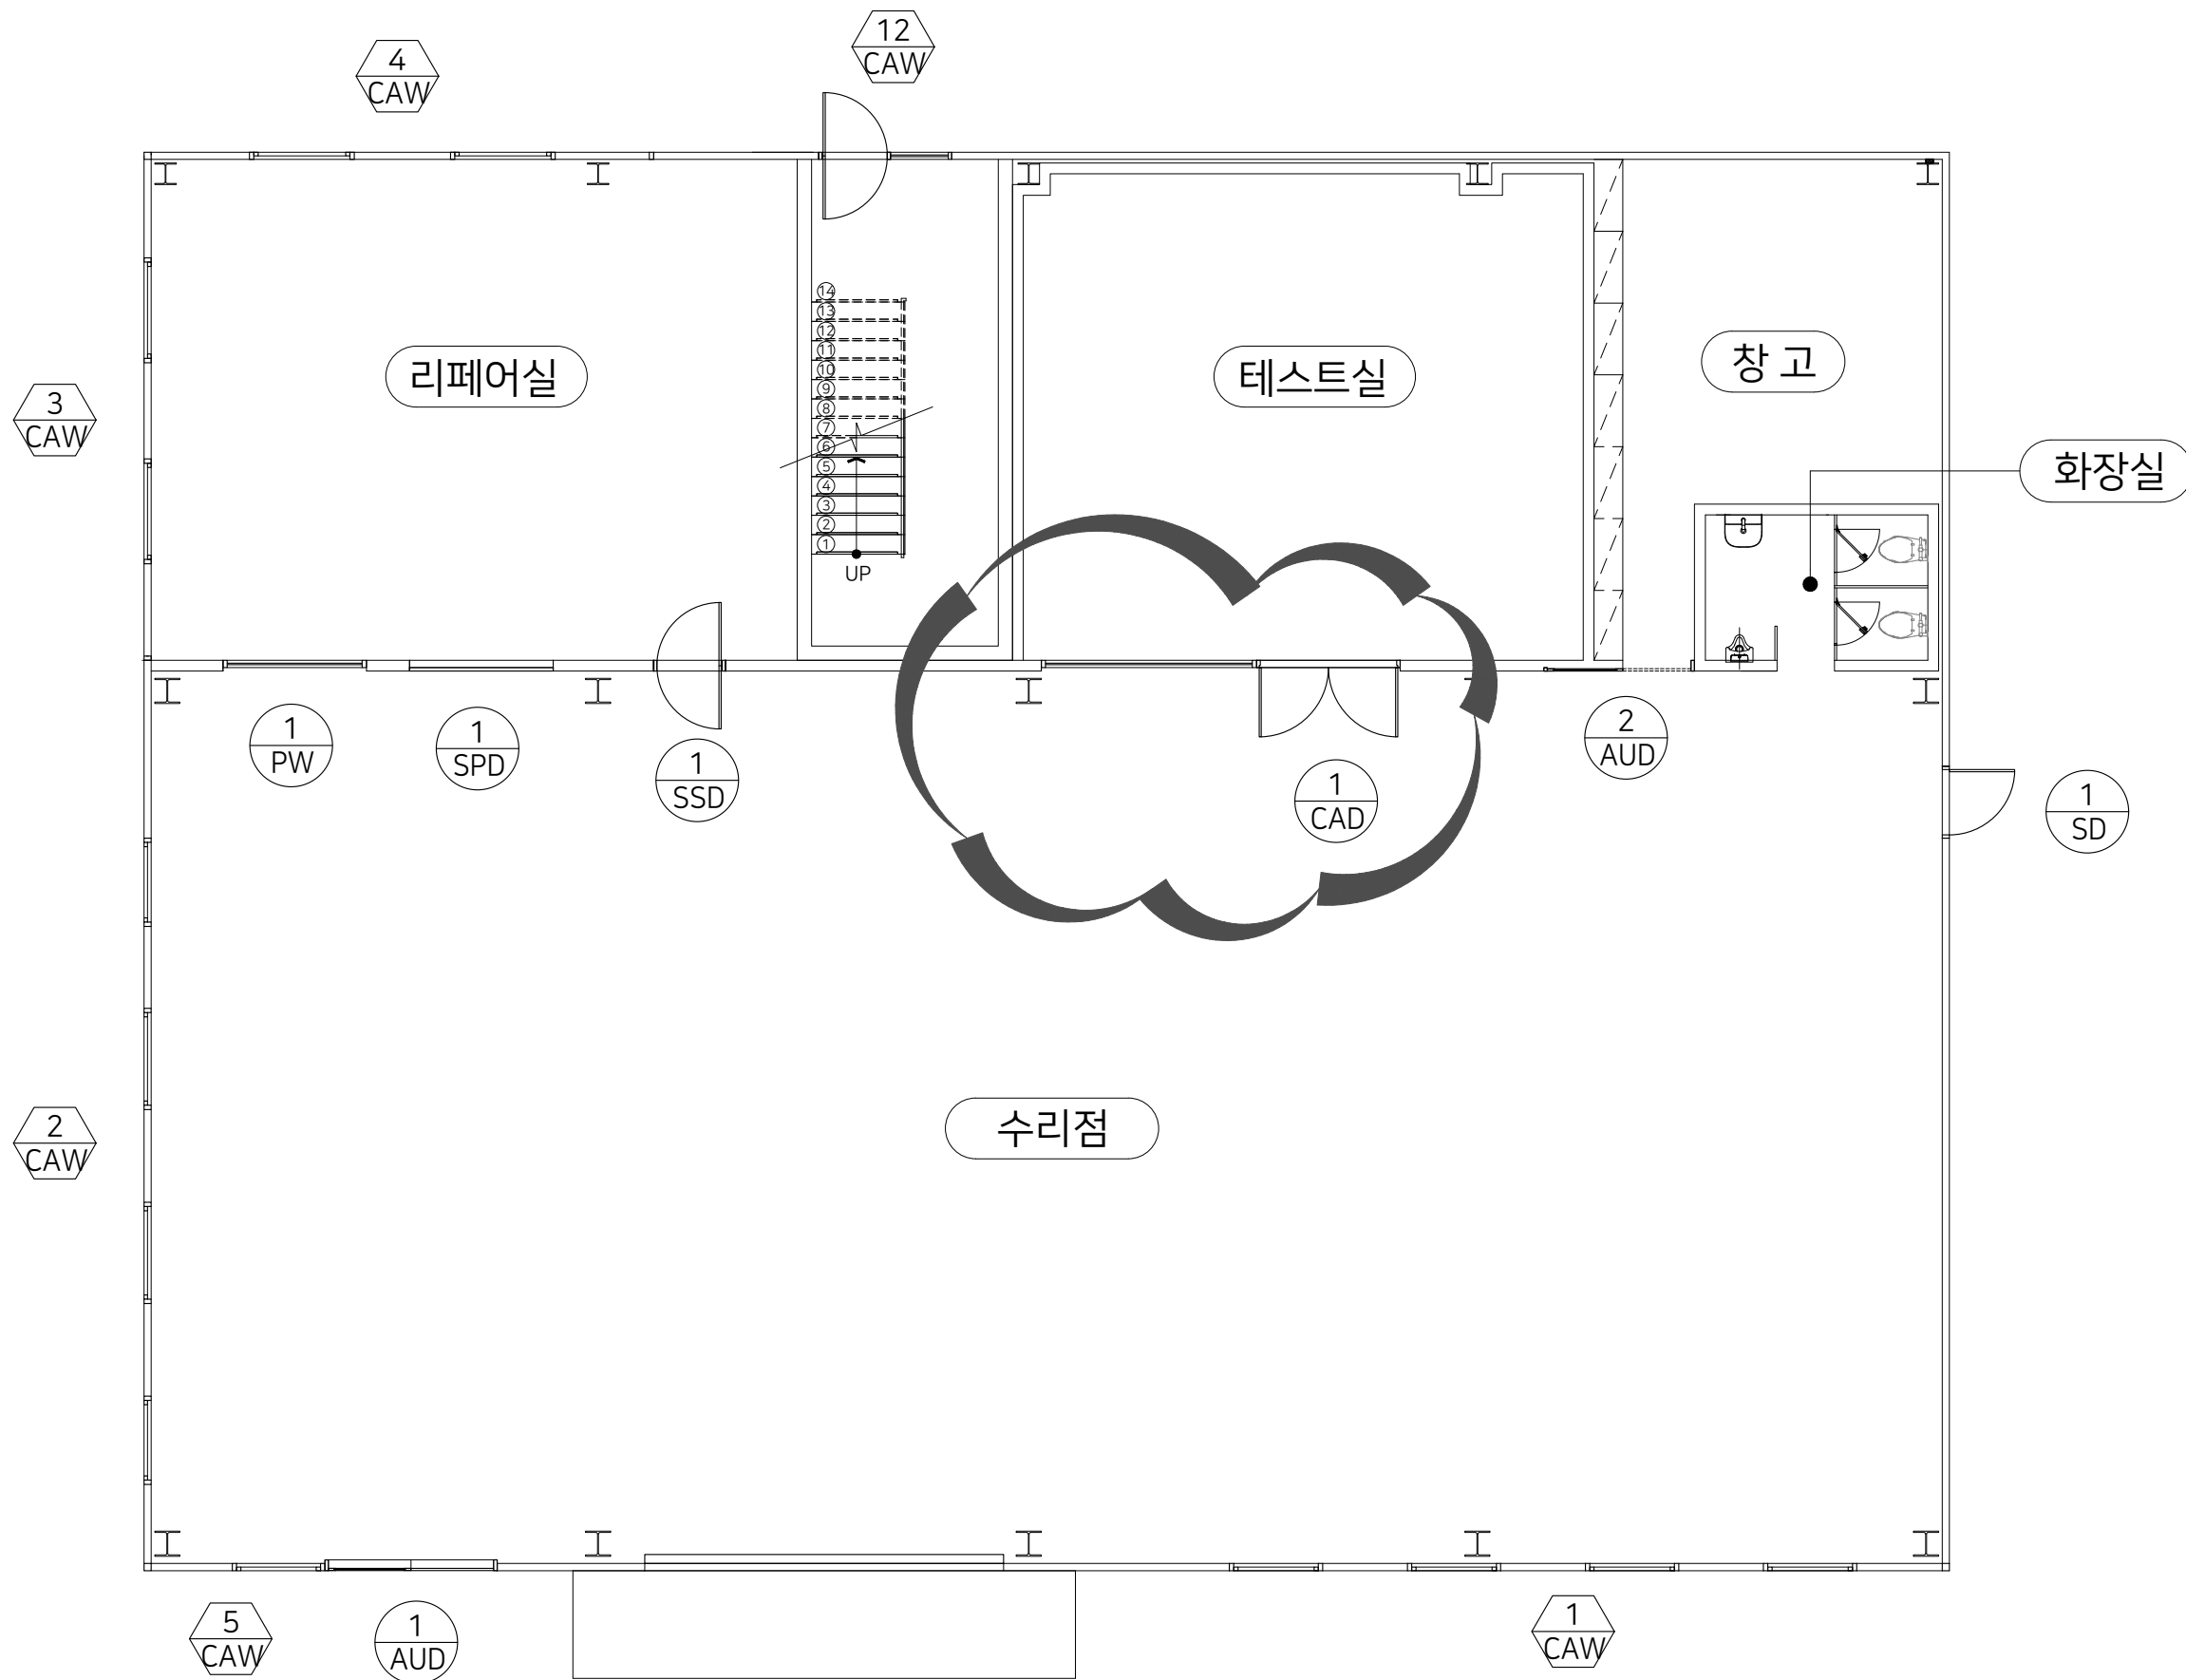

PROJECT TITLE
신진유압
화목동 698-14
신축계획안

PROJECT NO.

지음
건축사사무소
Architects & Interio

부산광역시 사하구 하단동 476
TEL . 051 . 791 . 0201
FAX . 051 . 791 . 0203

NOTE

NO.	REVISIONS / ISSUE	

ARCHITECTURE DESIGNED BY

STRUCTURE DESIGNED BY

MECHANICAL DESIGNED BY

DRAWN BY

CHECKED BY

APPROVED BY

NAME OF DRAWING

1층 창호부호도

SCALE

A1 SIZE

A3 SIZE 1 /


DATE 2026

DRAWING NO.

1층 창호부호도

1 A101

SCALE _ A1 1 / 75 , A3 1 / 150

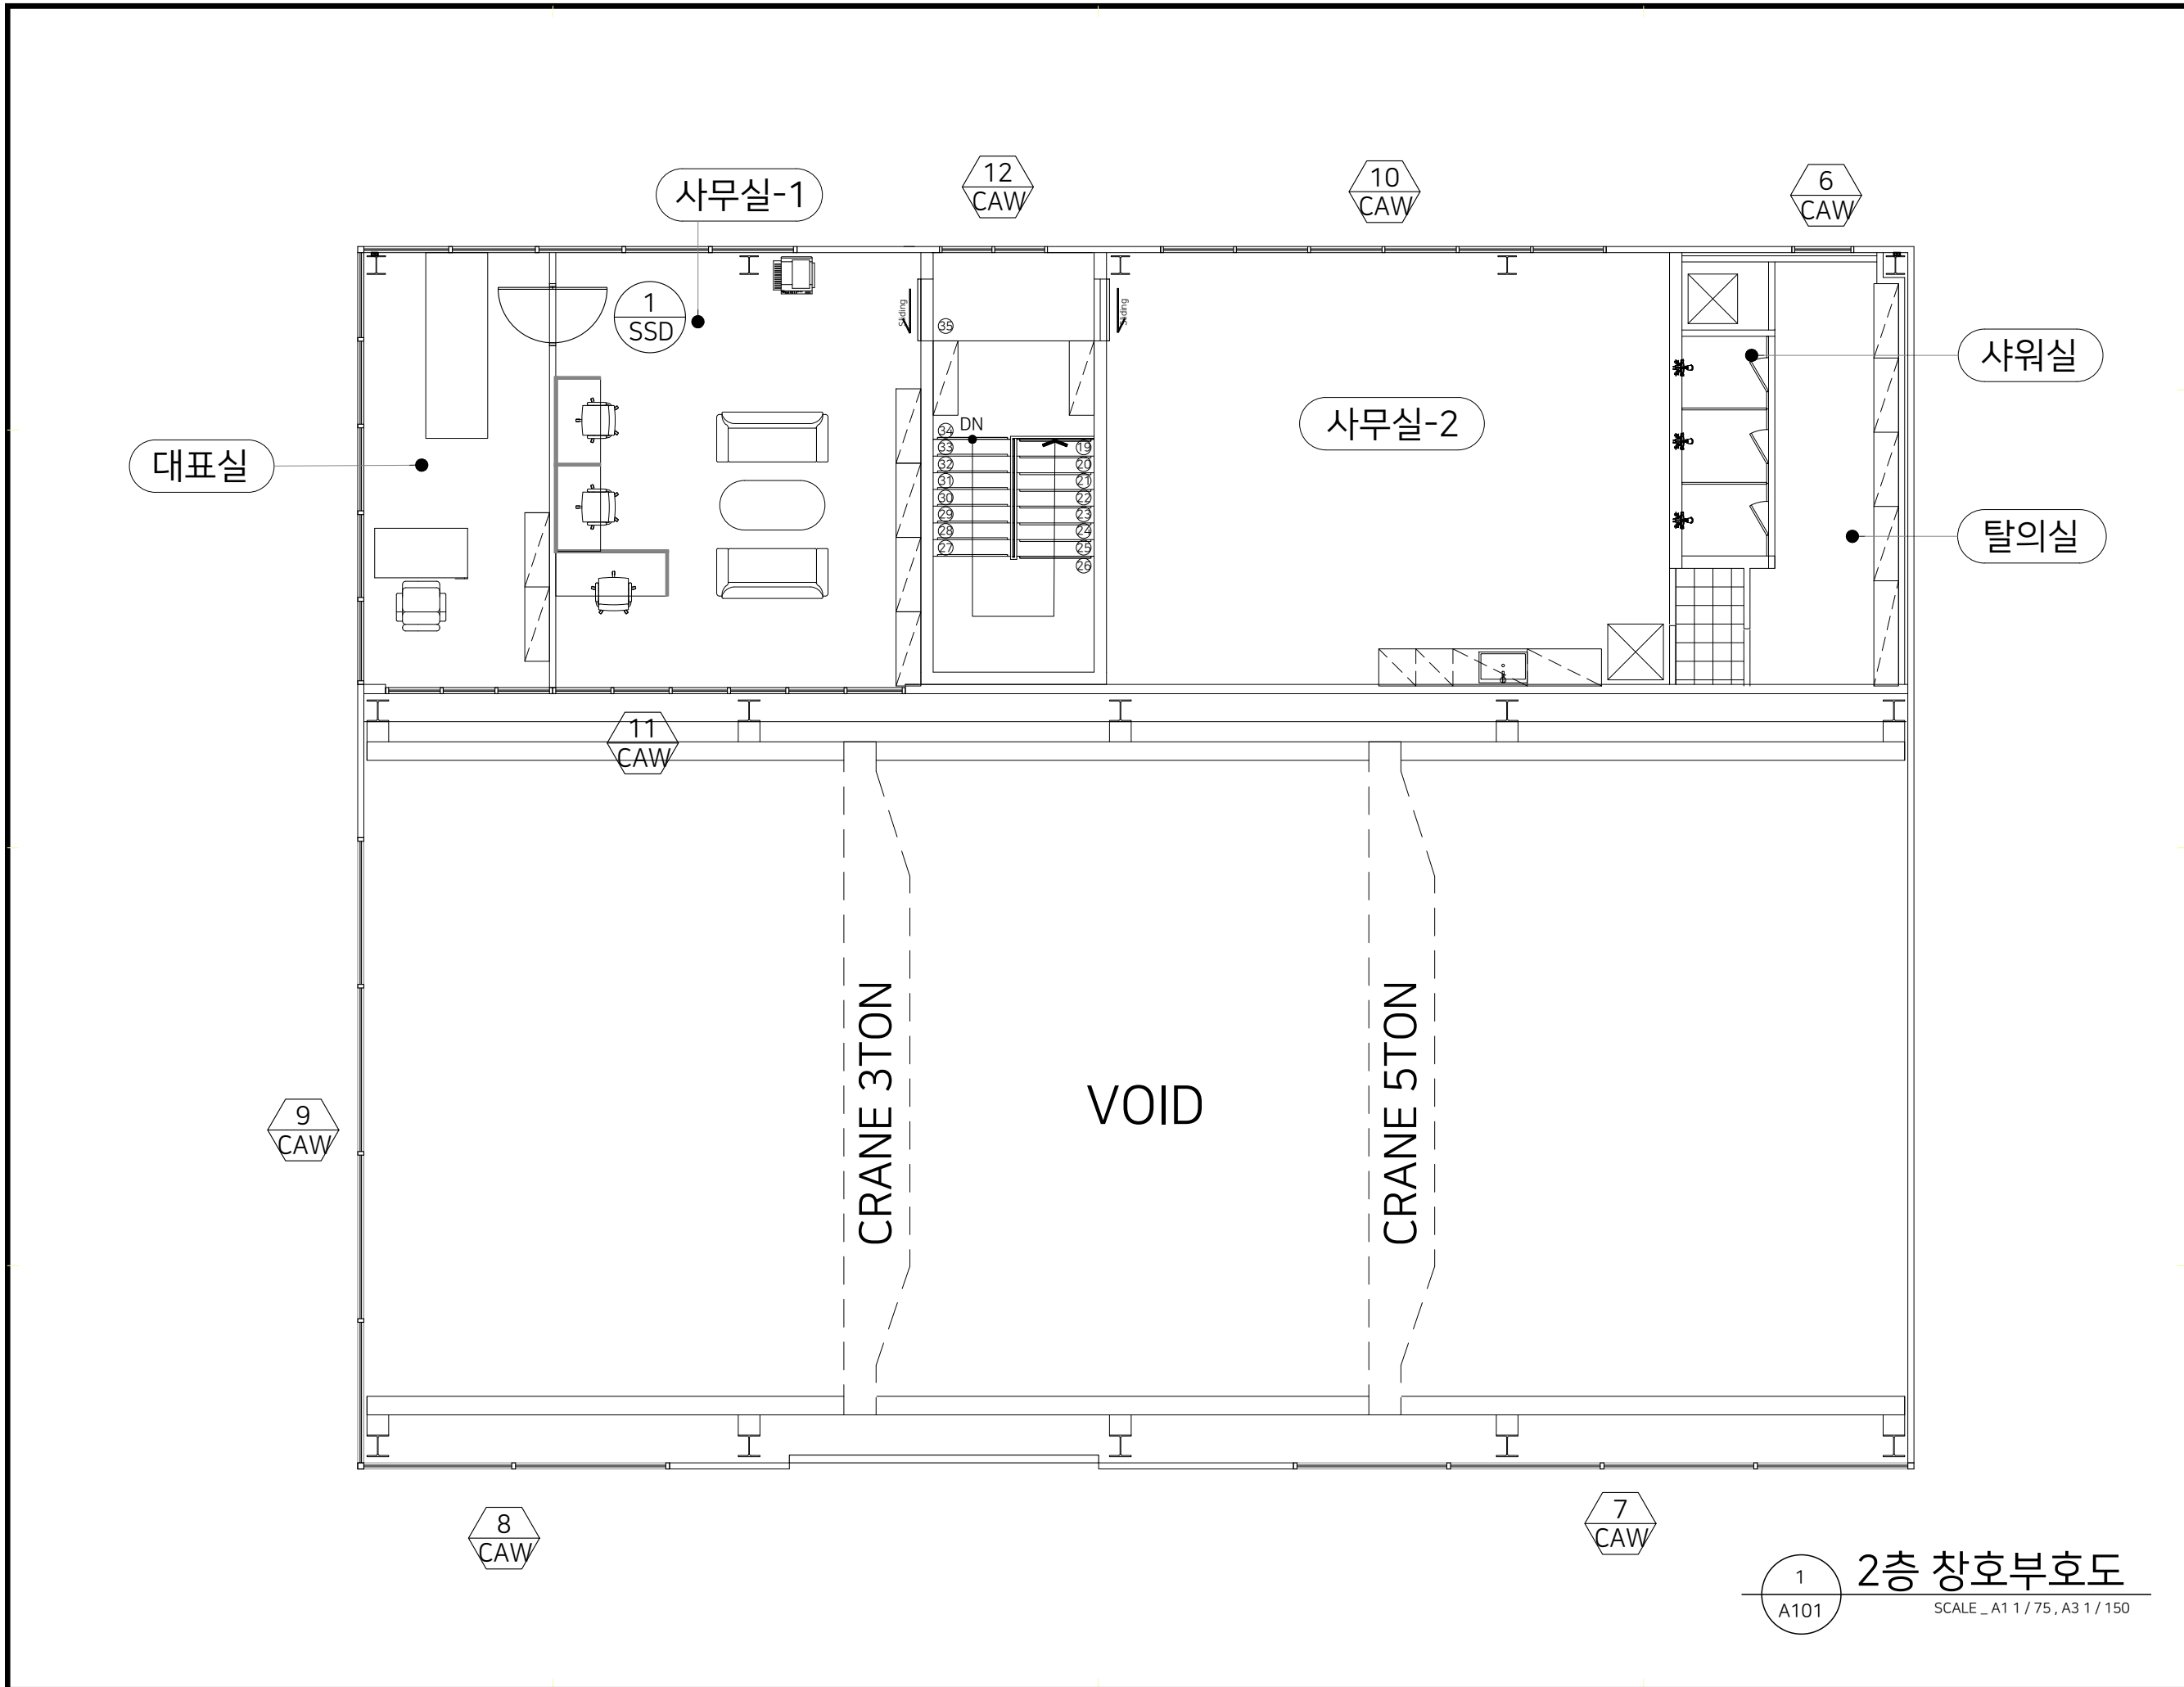

PROJECT TITLE

신진유압
화목동 698-14
신축계획안

PROJECT NO.

지음
건축사사무소
Architects & Interiors

부산광역시 사하구 하단동 476
TEL . 051 . 791 . 0201
FAX . 051 . 791 . 0203

NOTE

NO.	REVISIONS / ISSUE	

ARCHITECTURE DESIGNED BY

STRUCTURE DESIGNED BY

MECHANICAL DESIGNED BY

DRAWN BY

CHECKED BY

APPROVED BY

NAME OF DRAWING

2층 창호부호도

SCALE

A1 SIZE

A3 SIZE 1 /

DATE 2026

DRAWING NO.

1
A101

2층 창호부호도

SCALE _ A1 1 / 75 , A3 1 / 150

1 창호일람표-1 SCALE _ A1 1 / 50 A3 1 / 100										PROJECT TITLE									
부 호		1AUD칼라알루미늄 자동문			2AUD칼라알루미늄 자동문			3AUD칼라알루미늄 자동문			1SPD스피드도어		PROJECT NO.						
위 치		1층 수리점			1 개소	1층 창고			1 개소	2층 사무실-1, 사무실-2			2 개소	1층 테스트실			1 개소		
형 태																			
문 틀		THK125 AL.FRAME 위 불소수지코팅				THK125 AL.FRAME 위 불소수지코팅				THK125 AL.FRAME 위 불소수지코팅				스피드도어 상세도 참조					
유 리		THK12 투명강화유리				THK12 투명강화유리				THK12 투명강화유리				스피드도어 상세도 참조					
마 감		불소수지코팅(건축주지정컬러)				불소수지코팅(건축주지정컬러)				불소수지코팅(건축주지정컬러)				스피드도어 상세도 참조					
부 속 철 물		부속철물일체				부속철물일체				부속철물일체				부속일체 제작자 일식					
부 호		1SD철재 외여닫이문								1SSD스텐레스스틸 도어									
위 치		1층- 수리점 (우측면)			1 개소					1층- 리페어실, 2층 - 대표실			2 개소						
형 태																			
문 틀		지정제품사양(기성품)								THK150 SST FRAME 위 불소수지코팅									
유 리		-								THK12 투명강화유리									
마 감		지정제품사양(기성품)								불소수지코팅(건축주지정컬러)									
부 속 철 물		건축주지정 레버형손잡이, 부속철물일체								손잡이, 잠금장치 외 부속철물일체									
부 호																			
위 치																			
형 태																			
문 틀																		양면 0.5mm 아연도 강판 / 폴리우레탄 충진 50T	
유 리																		2중 ARCYLIC 투시창	
마 감																		엠포싱 처리 후 폴리에스터 마감	
부 속 철 물																		부속철물 제작자 일식	

지음

건축사사무소

Architects & Interio

부산광역시 사하구 하단동 476
TEL . 051 . 791 . 0201
FAX . 051 . 791 . 0203

NOTE

1.모든 창호는 시공전 실측하여 SHOP DRAW후 감리자의 승인을 득한후 제작 시공할 것.
2.유리와 창호프레임의 재질과 색상은 감리자의 승인을 득한후 제작 시공할 것.
3.마감차이에 의한 고임재는 별도 설치할 것.
4.창 OPEN부분은 방충망을 설치할 것.
5.창또는 문과 함께 설치되어지는 공들 폭은 마감두께를 고려하여 현장실측후 조절 가능.
6.열관류율 및 기밀성능
-외기에 직접면한 창호(공동주택외) : 1.8W/mK이하 적용.
-외기에 직접 면한 거실부위 창호의 기밀성능은 KS F2292 기밀성능시험 방법에 의해 그 성능이 2등급 이하 시공.
* 2등급(통기량1~1.99m³/hm²)
7.갑 : 60분+방화문 (비차열 1시간이상) 외기에 접한 단열조치 대상인 문은 단열두께 20mm이상, 열교차단재 적용제품으로 시공.
8.풍하중을 고려한 환기창 부속철물을 사용 할 것.
9.창호도에 명시되지 않은 사항은 반드시 감리 확인승인후 시공할 것.

NO.

REVISONS / ISSUE

0

ARCHITECTURE DESIGNED BY

STRUCTURE DESIGNED BY

MECHANICAL DESIGNED BY

DRAWN BY

CHECKED BY

APPROVED BY

NAME OF DRAWING

창호일람표

SCALE

A1 SIZE

A3 SIZE 1 /

DATE 2026

DRAWING NO.

A3

1 창호일람표-2				PROJECT TITLE	
부 호	1 칼라알루미늄 히든바 고정창 및 프로젝트창		2	칼라알루미늄 히든바 고정창 및 프로젝트창	
위 치	1층 정면 - 수리점		1 개소	1층 좌측면 - 수리점	
형 태			1 개소		
문 틀	THK100 AL.FRAME 위 불소수지코팅			THK100 AL.FRAME 위 불소수지코팅	
유 리	THK24 GRAY로이복층유리(THK5로이유리 소프트코팅+THK14아르곤+THK5 GRAY 유리)			THK24 GRAY로이복층유리(THK5로이유리 소프트코팅+THK14아르곤+THK5 GRAY 유리)	
마 감	DARK GREY COLOR _ 불소수지코팅			DARK GREY COLOR _ 불소수지코팅	
부 속 철 물	기본핸들1조 외 부속철물일체			기본핸들1조 외 부속철물일체	
부 호	3 칼라알루미늄 히든바 고정창 및 프로젝트창		4	칼라알루미늄 히든바 고정창 및 프로젝트창	
위 치	1층 좌측면 - 리페어실			1층 배면 - 리페어실	
형 태					
문 틀	THK100 AL.FRAME 위 불소수지코팅			THK100 AL.FRAME 위 불소수지코팅	
유 리	THK24 GRAY로이복층유리(THK5로이유리 소프트코팅+THK14아르곤+THK5 GRAY 유리)			THK24 GRAY로이복층유리(THK5로이유리 소프트코팅+THK14아르곤+THK5 GRAY 유리)	
마 감	DARK GREY COLOR _ 불소수지코팅			DARK GREY COLOR _ 불소수지코팅	
부 속 철 물	기본핸들1조 외 부속철물일체			기본핸들1조 외 부속철물일체	
부 호					
위 치					
형 태					
문 틀	THK100 AL.FRAME 위 불소수지코팅			THK100 AL.FRAME 위 불소수지코팅	
유 리	THK24 GRAY로이복층유리(THK5로이유리 소프트코팅+THK14아르곤+THK5 GRAY 유리)			THK24 GRAY로이복층유리(THK5로이유리 소프트코팅+THK14아르곤+THK5 GRAY 유리)	
마 감	DARK GREY COLOR _ 불소수지코팅			DARK GREY COLOR _ 불소수지코팅	
부 속 철 물	기본핸들1조 외 부속철물일체			기본핸들1조 외 부속철물일체	

지음

건축사사무소

Architects & Interio

부산광역시 사하구 하단동 476

TEL . 051 . 791 . 0201

FAX . 051 . 791 . 0203

- NOTE
- 1.모든 창호는 시공전 실측하여 SHOP DRAW후 감리자의 승인을 득한후 제작 시공할 것.

2.유리와 창호프레임의 재질과 색상은 감리자의 승인을 득한후 제작 시공할 것.

3.마감차이에 의한 고임재는 별도

4. 창 OPEN부분은 방충망을 설치할 것.

5.창또는 문과 함께 설치되어지는 공틀 쪽은 마감두께를 고려하여 현장실측후

6. 열관류율 및 기밀성능
-외기에 직접 면한 거실부위 창호의 기밀성능은 KS F2292 기밀성능시험 방법에 의해 그 성능이 2등급 이하 시공.
* 2등급(통기량1~1.99m³/hm²)

7. 갑 : 60분+방화문 (비차열 1시간이상) 외기에 접한 단열조치 대상인 문은 단열두께 20mm이상, 열교차단재 적용제품으로 시공.

8. 풍하중을 고려한 환기창 부속철물을

9. 창호도에 명시되지 않은 사항은 반드시 감리 확인승인후 시공할 것.

NO.	REVISIONS / ISSUE	

ARCHITECTURE DESIGNED BY

STRUCTURE DESIGNED BY

MECHANICAL DESIGNED BY

DRAWN BY

CHECKED BY

APPROVED BY

NAME OF DRAWING

창호일람표

SCALE

A1 SIZE

A3 SIZE

DATE

DRAWING NO.

1 / 1

2026

A3

1 창호일람표-3 SCALE _ A1 1 / 50 A3 1 / 100				PROJECT TITLE
부 호	5 SAW 칼라알루미늄 히든바 고정창 및 프로젝트창	6 SAW 칼라알루미늄 히든바 고정창 및 프로젝트창	7 SAW 칼라알루미늄 히든바 고정창	PROJECT NO.
위 치	1층 정면 - 수리점	2층 배면 - 탈의실	2층 정면 - 수리점	
형 태				NOTE 1.모든 창호는 시공전 실측하여 SHOP DRAW후 감리자의 승인을 득한후 제작 시공할 것. 2.유리와 창호프레임의 재질과 색상은 감리자의 승인을 득한후 제작 시공할 것. 3.마감차이에 의한 고임재는 별도 설치할 것. 4.창 OPEN부분은 방충망을 설치할 것. 5.창또는 문과 함께 설치되어지는 공물 쪽은 마감두께를 고려하여 현장실측후 조절 가능. 6.열관류율 및 기밀성능 -외기에 직접면한 창호(공동주택외) : 1.8W/mK이하 적용. -외기에 직접 면한 거실부위 창호의 기밀성능은 KS F2292 기밀성능시험 방법에 의해 그 성능이 2등급 이하 시공. * 2등급(통기량1~1.99m³/hm²) 7.갑 : 60분+방화문 (비차열 1시간이상) 외기에 접한 단열조치 대상인 문은 단열두께 20mm이상, 열교차단재 적용제품으로 시공. 8.풍하중을 고려한 환기창 부속철물을 사용 할 것. 9.창호도에 명시되지 않은 사항은 반드시 감리 확인승인후 시공할 것.
	▼ SL	▼ SL	▼ SL	
	문 틀	THK100 AL.FRAME 위 불소수지코팅	THK100 AL.FRAME 위 불소수지코팅	
	유 리	THK24 GRAY로이복층유리(THK5로이유리 소프트코팅+THK14아르곤+THK5 GRAY 유리)	THK24 GRAY로이복층유리(THK5로이유리 소프트코팅+THK14아르곤+THK5 GRAY 유리)	
	마 감	DARK GREY COLOR _ 불소수지코팅	DARK GREY COLOR _ 불소수지코팅	
부 속 철 물	기본핸들1조 외 부속철물일체	기본핸들1조 외 부속철물일체	기본핸들1조 외 부속철물일체	
부 호	8 SAW 칼라알루미늄 히든바 고정창	9 SAW 칼라알루미늄 히든바 고정창	12 SAW 칼라알루미늄 히든바 고정창 및 프로젝트창	
위 치	2층 배면 - 수리점	2층 배면 - 수리점	1층 정면 - 수리점	
형 태				
	▼ SL	▼ SL	▼ SL	
	문 틀	THK100 AL.FRAME 위 불소수지코팅	THK100 AL.FRAME 위 불소수지코팅	
	유 리	THK24 GRAY로이복층유리(THK5로이유리 소프트코팅+THK14아르곤+THK5 GRAY 유리)	THK24 GRAY로이복층유리(THK5로이유리 소프트코팅+THK14아르곤+THK5 GRAY 유리)	
	마 감	DARK GREY COLOR _ 불소수지코팅	DARK GREY COLOR _ 불소수지코팅	
부 속 철 물	기본핸들1조 외 부속철물일체	기본핸들1조 외 부속철물일체		
부 호	10 SAW 칼라알루미늄 히든바 고정창 및 프로젝트창	11 SAW 칼라알루미늄 히든바 고정창		
위 치	2층 배면 - 사무실-2	2층 배면 - 수리점		
형 태				
	▼ SL	▼ SL		
	문 틀	THK100 AL.FRAME 위 불소수지코팅	THK100 AL.FRAME 위 불소수지코팅	
	유 리	THK24 GRAY로이복층유리(THK5로이유리 소프트코팅+THK14아르곤+THK5 GRAY 유리)	THK24 GRAY로이복층유리(THK5로이유리 소프트코팅+THK14아르곤+THK5 GRAY 유리)	
	마 감	DARK GREY COLOR _ 불소수지코팅	DARK GREY COLOR _ 불소수지코팅	
부 속 철 물	기본핸들1조 외 부속철물일체	기본핸들1조 외 부속철물일체	기본핸들1조 외 부속철물일체	
문 틀	THK100 AL.FRAME 위 불소수지코팅	THK100 AL.FRAME 위 불소수지코팅	THK100 AL.FRAME 위 불소수지코팅	
유 리	THK24 GRAY로이복층유리(THK5로이유리 소프트코팅+THK14아르곤+THK5 GRAY 유리)	THK24 GRAY로이복층유리(THK5로이유리 소프트코팅+THK14아르곤+THK5 GRAY 유리)	THK24 GRAY로이복층유리(THK5로이유리 소프트코팅+THK14아르곤+THK5 GRAY 유리)	
마 감	DARK GREY COLOR _ 불소수지코팅	DARK GREY COLOR _ 불소수지코팅	DARK GREY COLOR _ 불소수지코팅	
부 속 철 물	기본핸들1조 외 부속철물일체	기본핸들1조 외 부속철물일체	기본핸들1조 외 부속철물일체	



부산광역시 사하구 하단동 476
TEL . 051 . 791 . 0201
FAX . 051 . 791 . 0203

- NOTE
- 1.모든 창호는 시공전 실측하여 SHOP DRAW후 감리자의 승인을 득한후 제작 시공할 것.
- 2.유리와 창호프레임의 재질과 색상은 감리자의 승인을 득한후 제작 시공할 것.
- 3.마감차이에 의한 고임재는 별도 설치할 것.
- 4.창 OPEN부분은 방충망을 설치할 것.
- 5.창또는 문과 함께 설치되어지는 공물 쪽은 마감두께를 고려하여 현장실측후 조절 가능.
- 6.열관류율 및 기밀성능
-외기에 직접면한 창호(공동주택외)
: 1.8W/mK이하 적용.
- 외기에 직접 면한 거실부위 창호의 기밀성능은 KS F2292 기밀성능시험 방법에 의해 그 성능이 2등급 이하 시공.
* 2등급(통기량1~1.99m³/hm²)
- 7.갑 : 60분+방화문 (비차열 1시간이상) 외기에 접한 단열조치 대상인 문은 단열두께 20mm이상, 열교차단재 적용제품으로 시공.
- 8.풍하중을 고려한 환기창 부속철물을 사용 할 것.
- 9.창호도에 명시되지 않은 사항은 반드시 감리 확인승인후 시공할 것.

NO.	REVISIONS / ISSUE	

ARCHITECTURE DESIGNED BY

STRUCTURE DESIGNED BY

MECHANICAL DESIGNED BY

DRAWN BY

CHECKED BY

APPROVED BY

NAME OF DRAWING

창호일람표

SCALE

A1 SIZE

A3 SIZE

DATE

DRAWING NO.